

暖阳颐养之家

社区嵌入式养老服务中心 · 室内设计方案
WARM SUN CARE HOME — An age-friendly interior for a two-storey community centre (3# Building)

让老去，被温柔地接住

设计方向

像家一样熟悉，比家更安心。

DESIGN DIRECTION

以暖木 · 奶油白 · 陶土 · 鼠尾草绿构成“家”的底色，用无感的适老细节守护尊严；让一栋规整的两层楼，成为有阳光、有邻里、有记忆的颐养之家。

温 Warm 安 Safe 明 Bright 忆 Memory 伴 Together

图纸解读


3.3m 柱距 × 8 + 6.6m 大厅

进深

居室 7.5m · 走廊 1.8m


转角翼

4 间 · 40° 折角

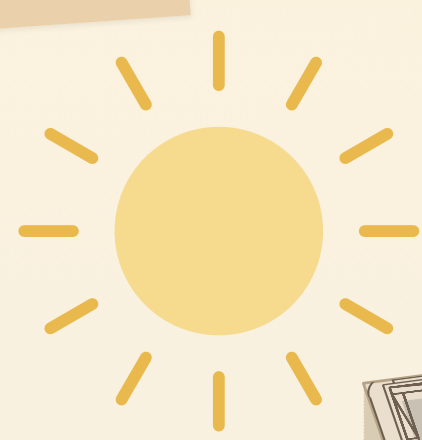

南向日光，整日相伴

二层 · 居住照护

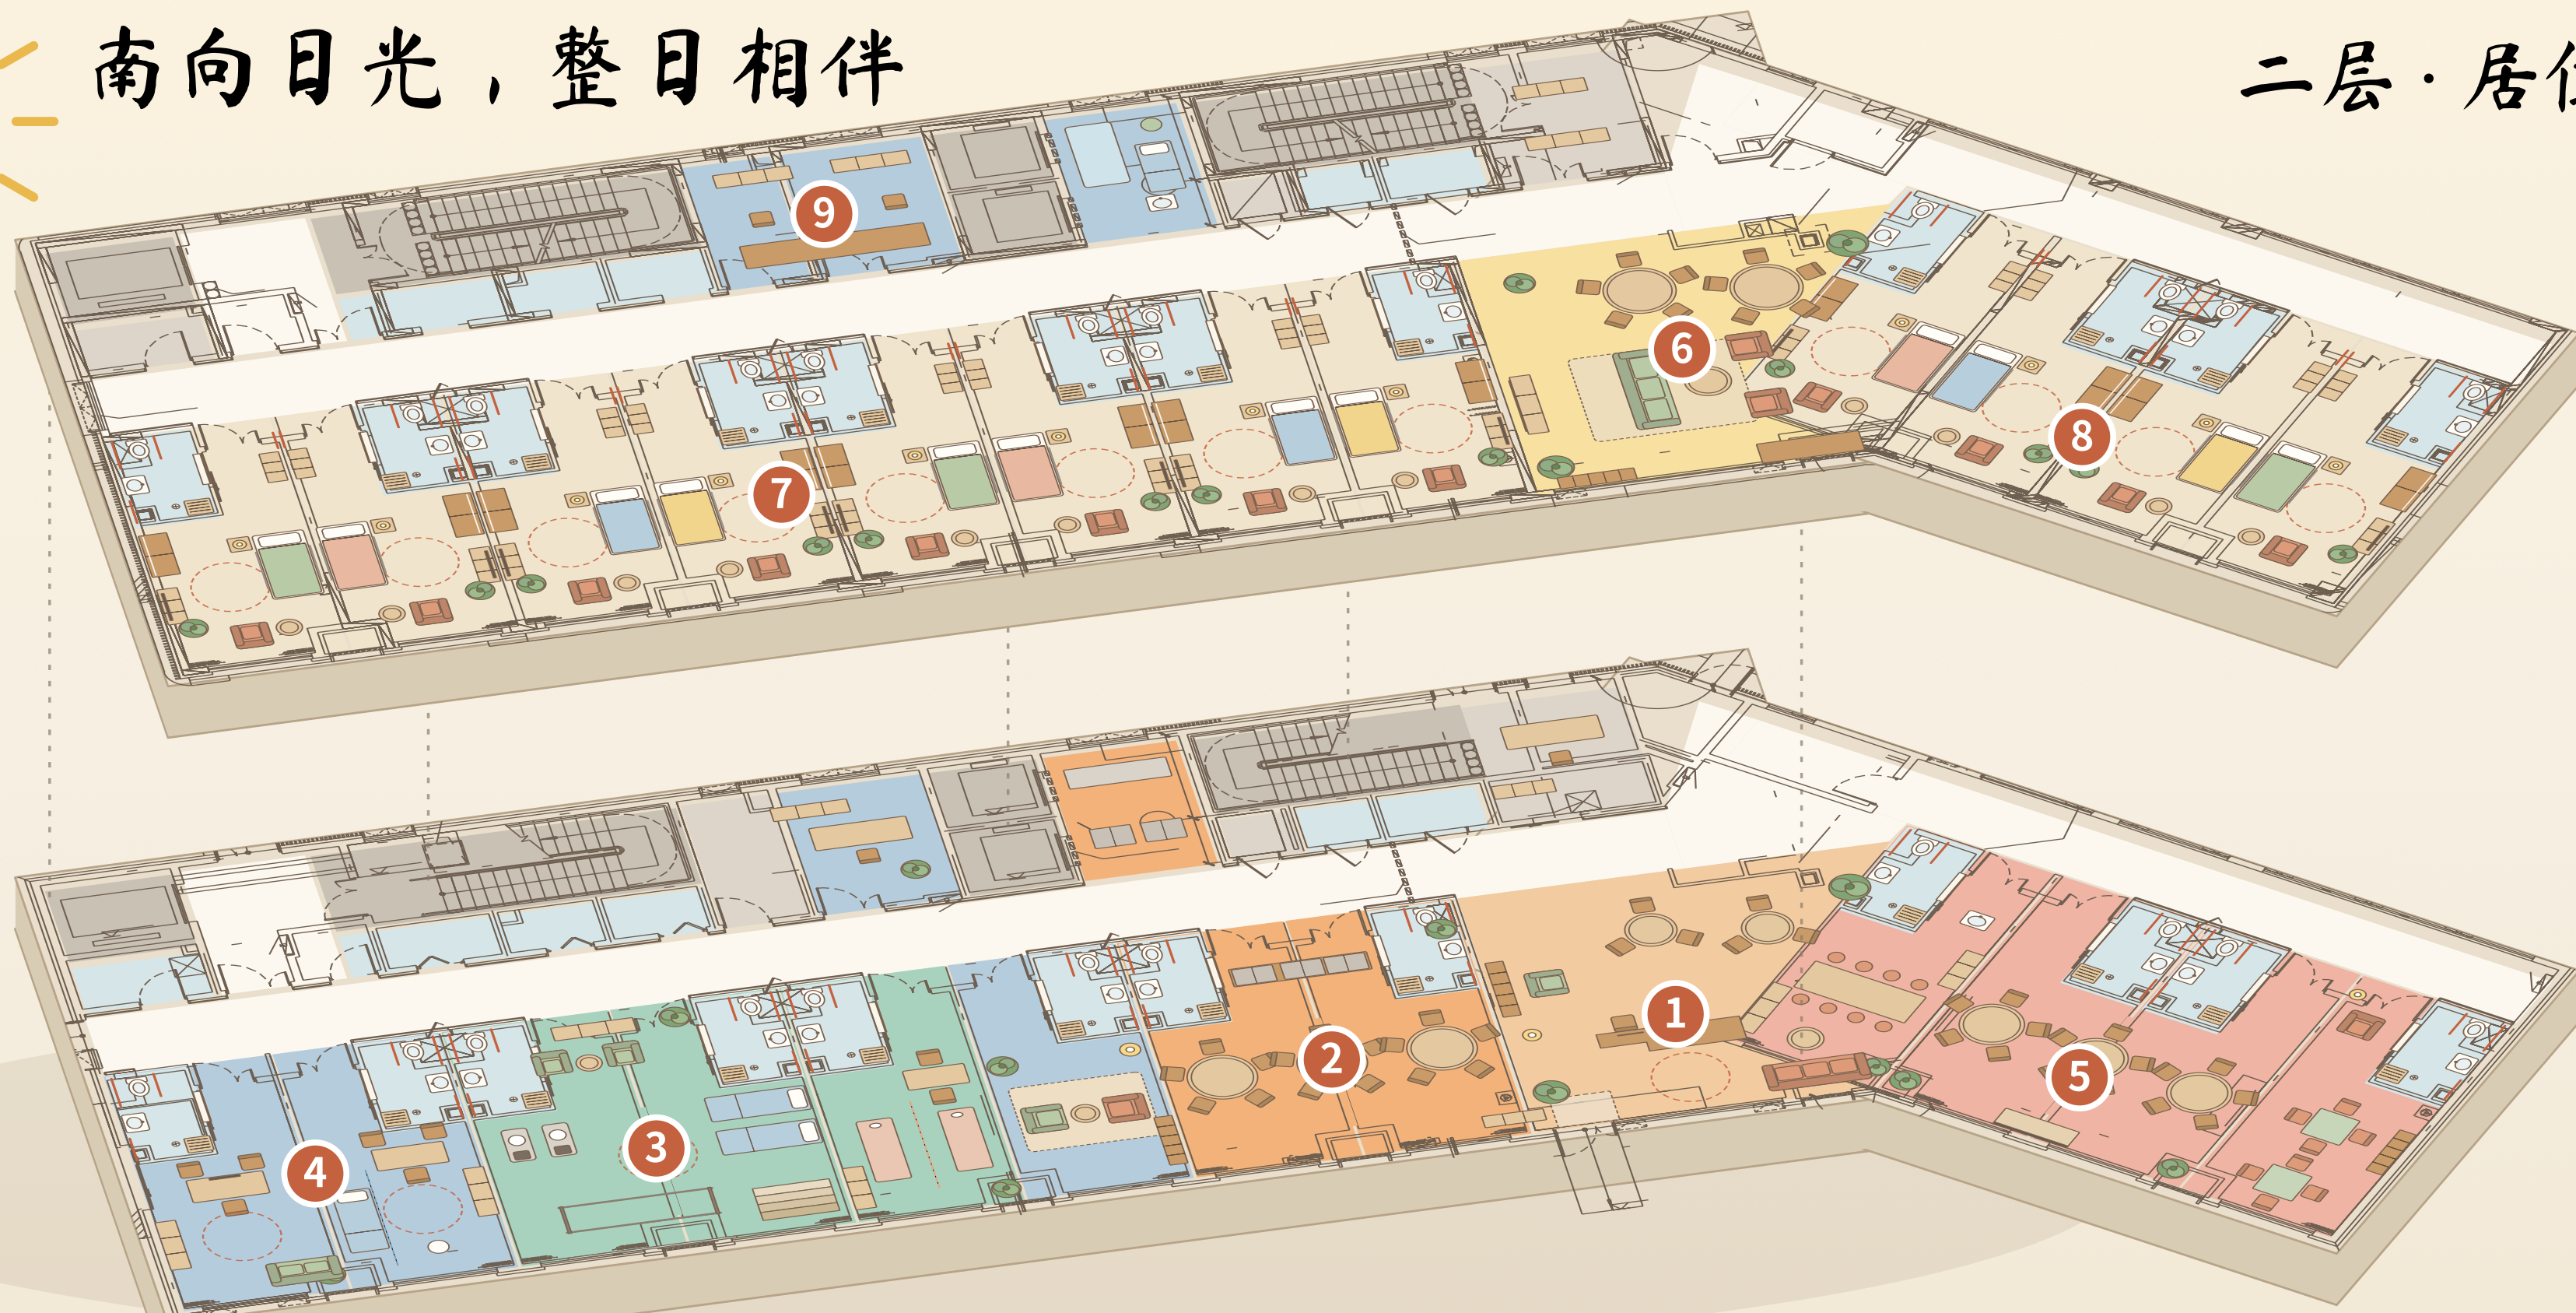

一层 · 公共服务

1 门厅 · 接待 · 茶座 2 长者食堂 3 康复训练室 4 医务 · 值班 5 多功能活动厅 6 日光起居 · 共享餐厅 7 居室 × 8 (朝南) 8 转角翼居室 × 4 9 护理站

分解轴测 EXPLODED AXONOMETRIC · 依据 3# 楼一、二层平面 1:100

01 设计理念

CONCEPT

图纸是一栋规整的两层楼：南侧 8 间 3.3m 开间单元、1.8m 中廊，东端 6.6m 大厅，再折出 4 间 40° 转角翼。

化整为零 一个开间即一间居室，保持“家”的尺度。

阳光向南 居室与日光厅全部朝南，整日有光。

公共在下，私密在上 一层接纳社区与康复，二层留给睡眠与陪伴。

去机构化 医疗设备隐入柜体，以家具、织物、灯具营造居家氛围。

02 适老五原则

FIVE PRINCIPLES

- 安 SAFE**
走廊净宽约 1.8m，双层连续扶手，无门槛、防滑地胶、家具全圆角
- 暖 WARM**
暖木 · 奶油白 · 陶土 · 鼠尾草绿；触感柔软，避免冷金属与强反光
- 明 BRIGHT**
南向自然光 + 3000K 暖白光；低眩光，夜间 0.25m 脚灯
- 忆 MEMORY**
门框色彩记忆条、“记忆盒”、廊内视觉地标，降低迷路焦虑
- 伴 TOGETHER**
居室 — 廊下座 — 日光厅 / 食堂，三级社交梯度

03 色彩与氛围


COLOUR & MOOD



暖色亲近，雾蓝静谧；晨光黄与陶土用作视觉地标。

04 功能分区


FUNCTION ZONING

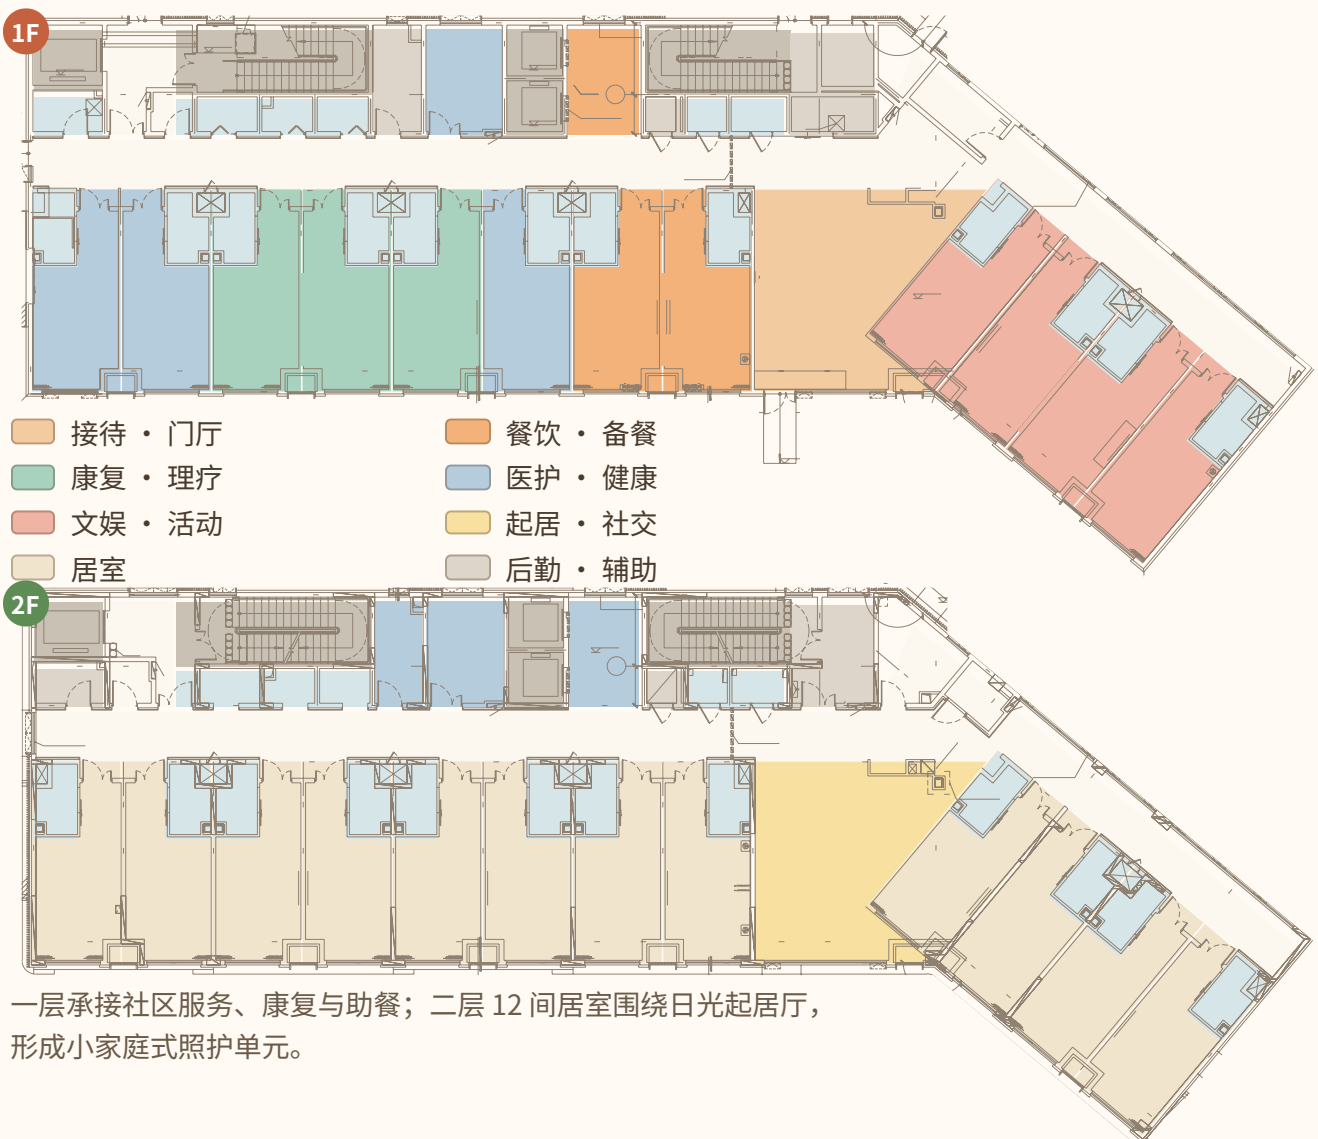

一层承接社区服务、康复与助餐；二层 12 间居室围绕日光起居厅，形成小家庭式照护单元。

05 动线分析


CIRCULATION

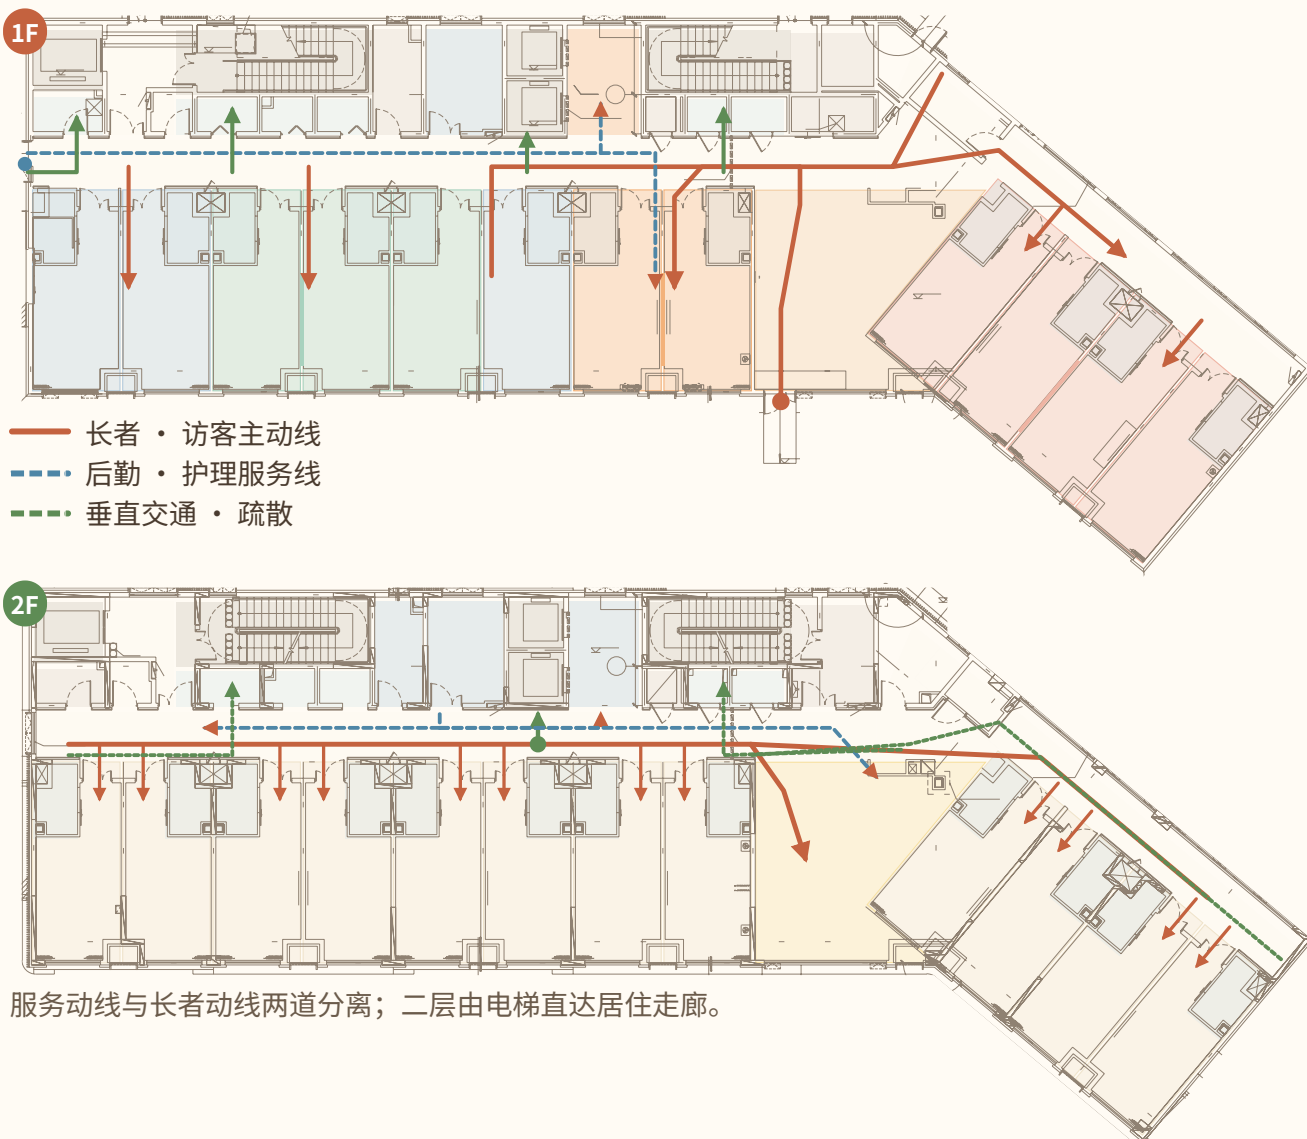

服务动线与长者动线两道分离；二层由电梯直达居住走廊。

06 光环境


LIGHT

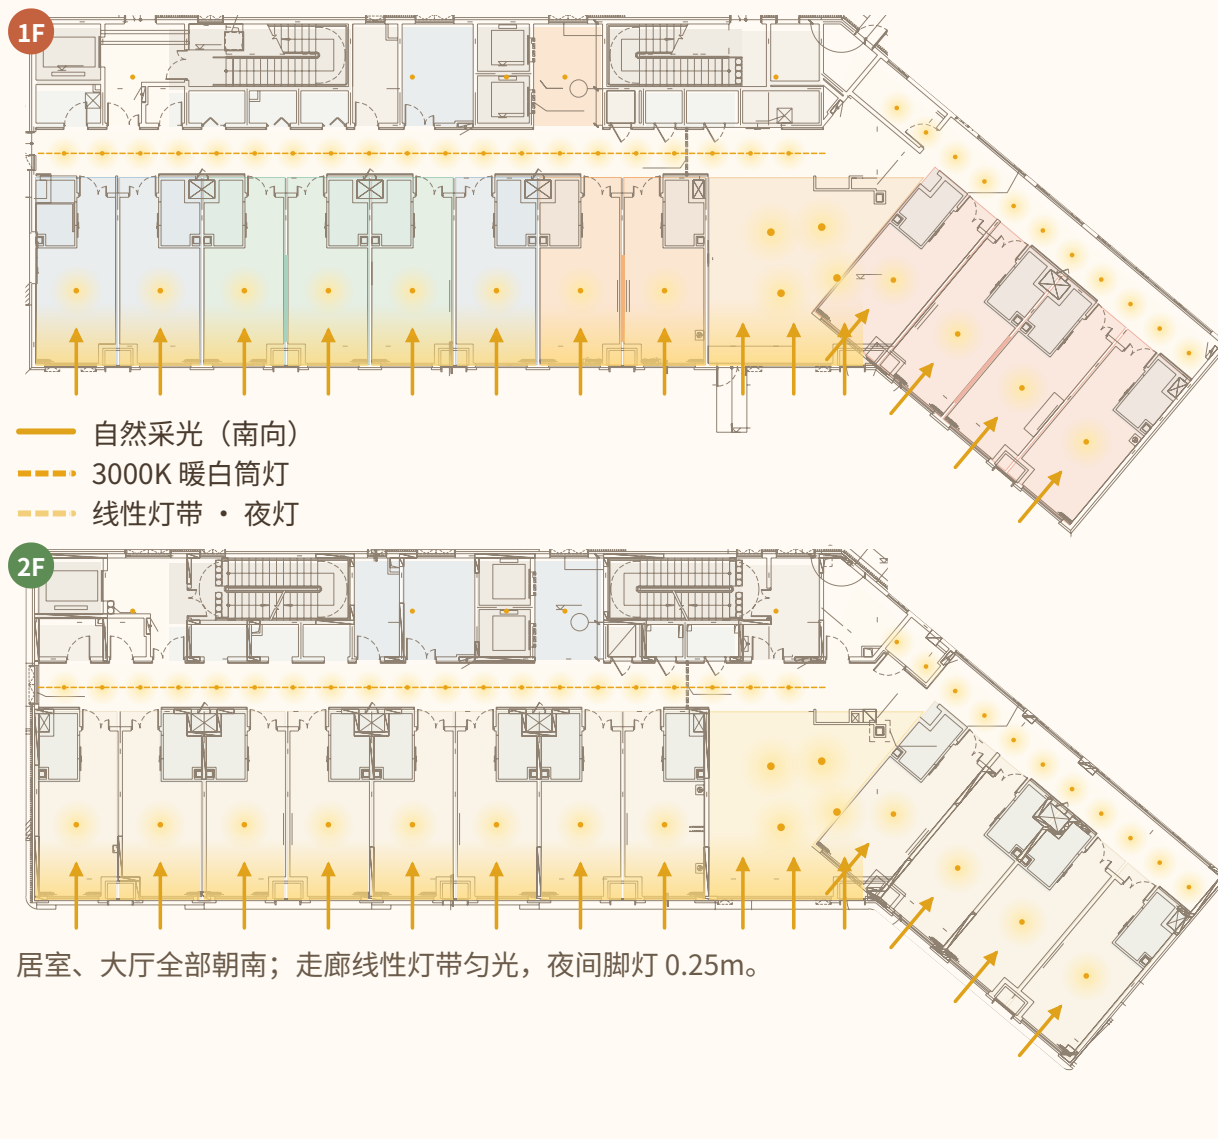

居室、大厅全部朝南；走廊线性灯带匀光，夜间脚灯 0.25m。

07 材质板

MATERIAL BOARD

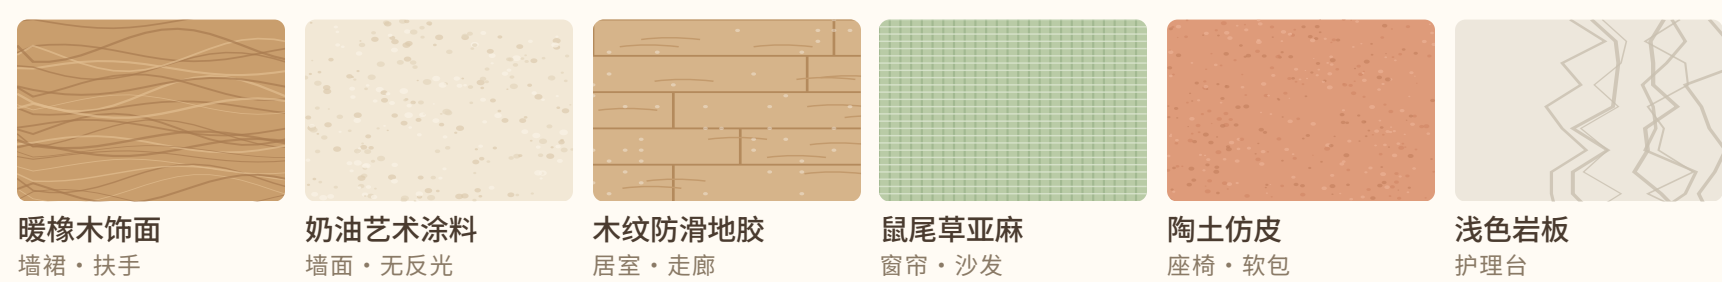

08 适老关键尺度

DIMENSIONS · MM

走廊净宽	≥ 1800	约 1.8m
居室门净宽	1000	含推拉门
连续扶手	650 / 850	双层
护理床面高	500	可调
轮椅回转	Ø1500	居室、卫生间
坐姿窗台	≤ 600	低窗台


09 项目指标

KEY FIGURES


2 层	12 间单人居室	≈ 1160 m² 总建筑面积
≈ 23.6 m²/间 (含卫)	1.8 m 走廊净宽	3.3 m 居室开间

10 空间意象

SPACE IMPRESSIONS · 示意插画

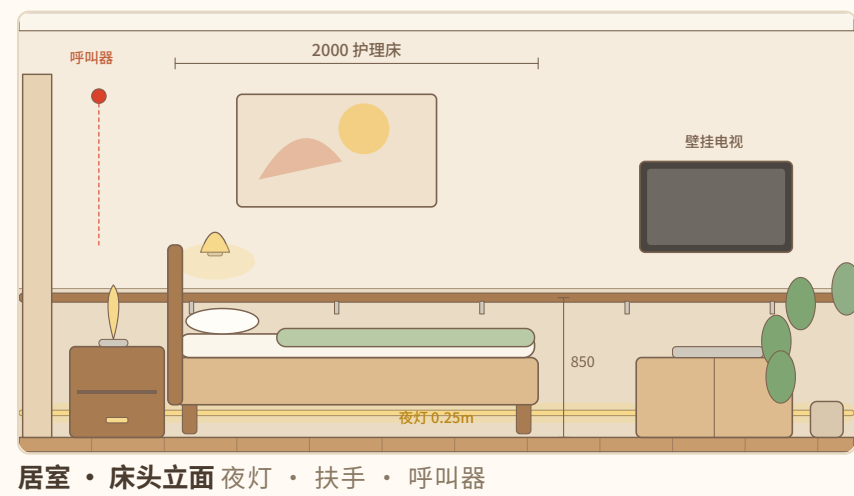


居室 · 床头立面 夜灯 · 扶手 · 呼叫器

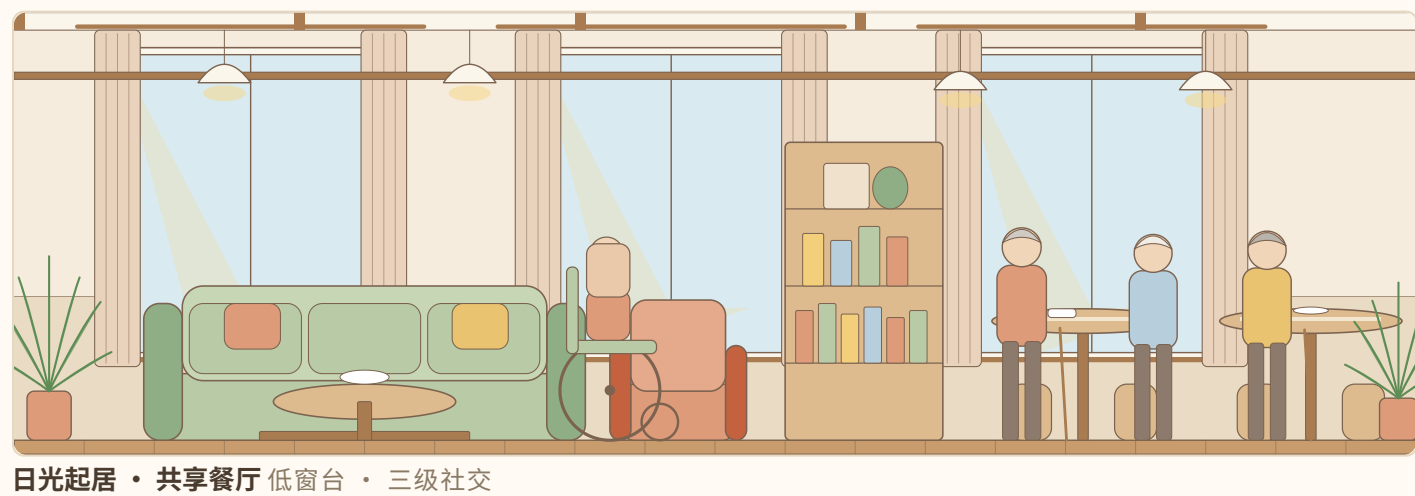

日光起居 · 共享餐厅 低窗台 · 三级社交



门厅 · 接待 低位台面 · 轮椅友好

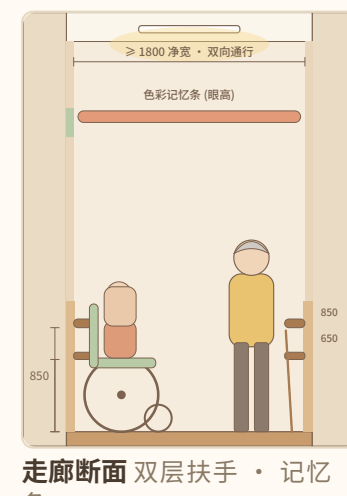

走廊断面 双层扶手 · 记忆条