

一层 · 公共服务层

接待 · 康复 · 医护 · 助餐 · 文娱

把社区请进来，让长者走出去

本层功能

- 接待 · 门厅
- 康复 · 理疗
- 文娱 · 活动

- 1 间 43.9㎡
- 2 间
- 3 间
- 医护 · 健康
- 餐饮 · 备餐
- 后勤 · 辅助

PROGRAMME

- 3 间
- 1 间 + 备餐间
- 服务核

功能用房约 327㎡；由南向坡道进入门厅，向西依次为医务、康复、理疗、谈话与食堂；向东转入 40° 翼的文娱空间。

坡道 → 门厅接待 → 廊道 → 康复 · 食堂 · 活动




设计要点 KEY MOVES

- 进得来 南向坡道 + 感应门，入口即门厅，一眼看清全层
- 走得稳 走廊双侧扶手、无高差、每12m设休息座
- 愿意留 康复、食堂、活动厅连成一串“愿意去的地方”
- 看得见 服务空间玻璃隔断，护理员视线覆盖公共区

一层平面图 GROUND FLOOR PLAN 1:90 (示意, 随排版比例)


A 功能分区

ZONING

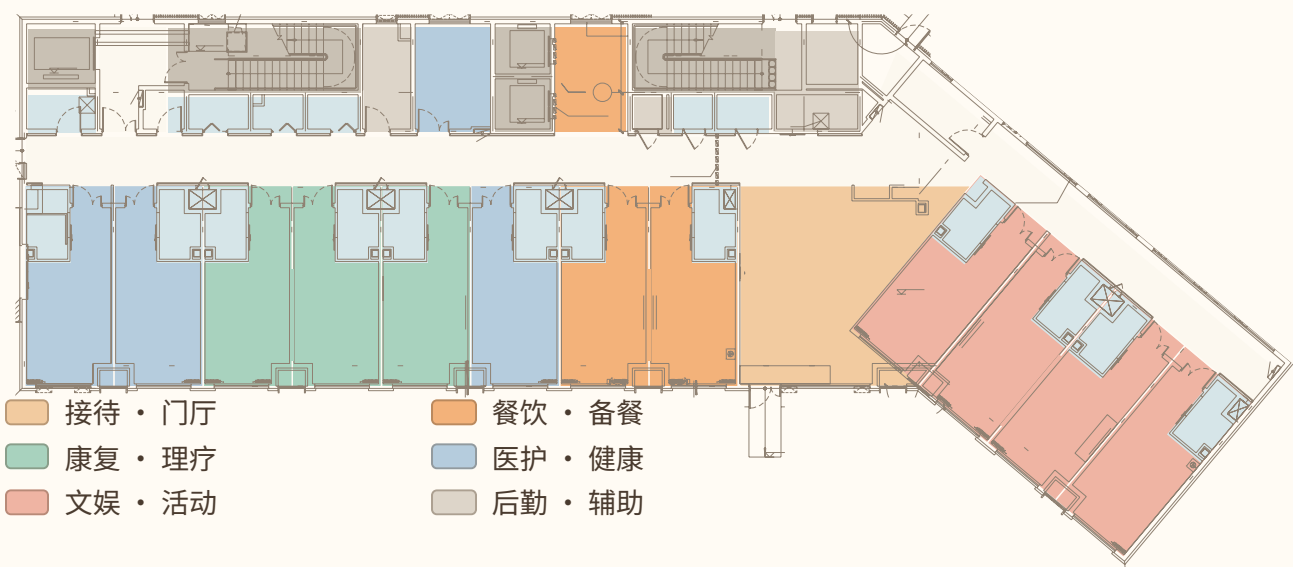

1 门厅 · 接待 · 茶座



LOBBY & TEA LOUNGE

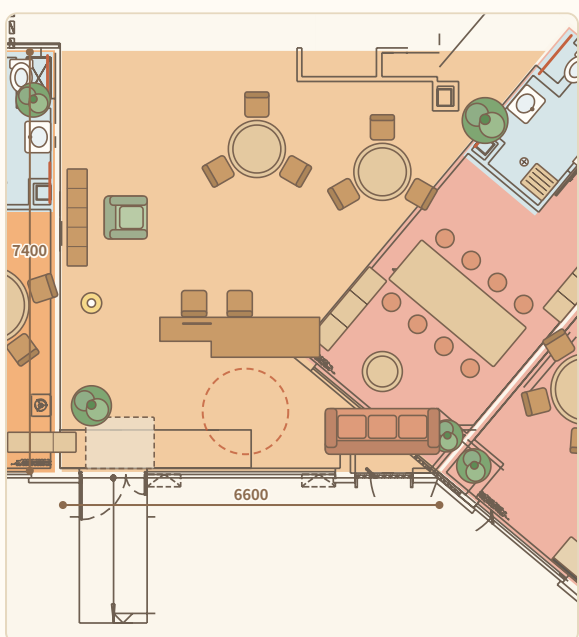

- 低位接待台一半 750mm，轮椅可近，可坐着服务
- 无高差入口：南向 1:12 缓坡 + 感应门净宽 ≥ 1200
- 日光茶座面向廊道，长者“看得见来往的人”

2 康复训练室



REHAB GYM

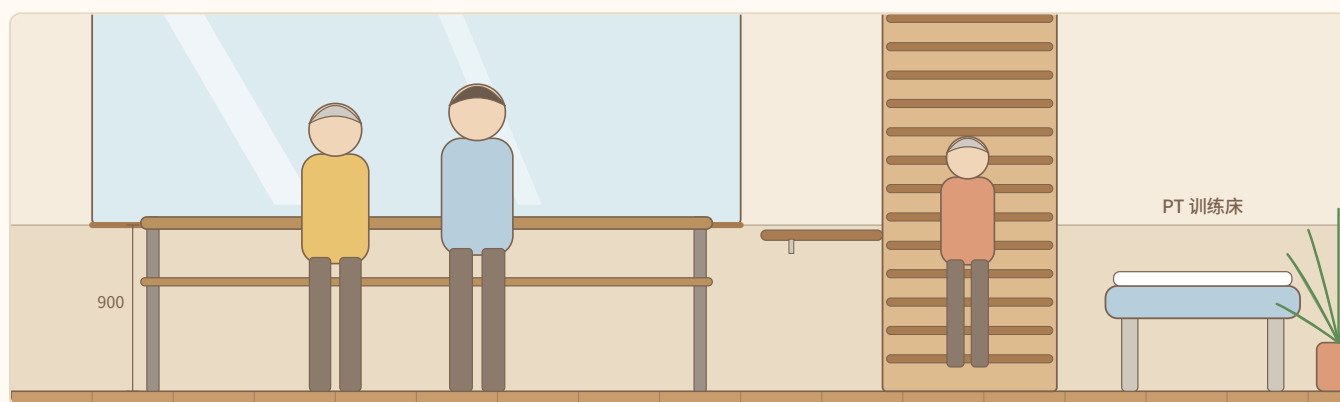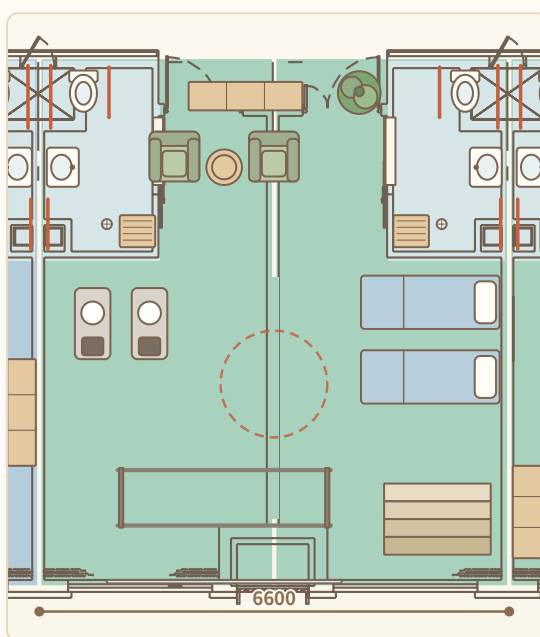

- 步行训练区：平行杠 + 落地镜；肋木、PT 训练床、上下楼训练
- 两开间打通，约 47㎡，可同时 6-8 人训练
- 弹性防滑地胶，墙面 0.9m 起扶手贯通

3 长者食堂 · 助餐



COMMUNITY CANTEN

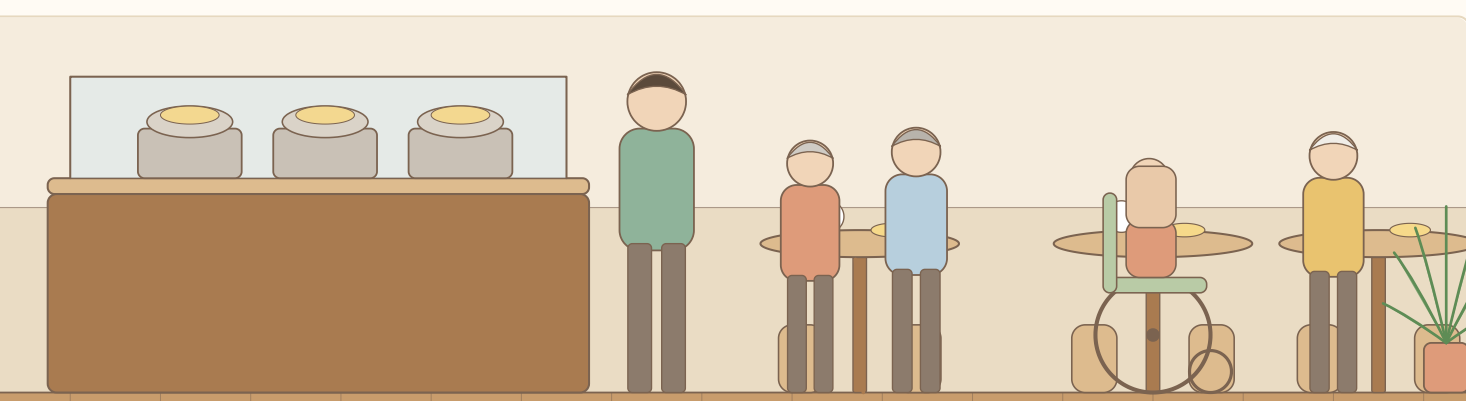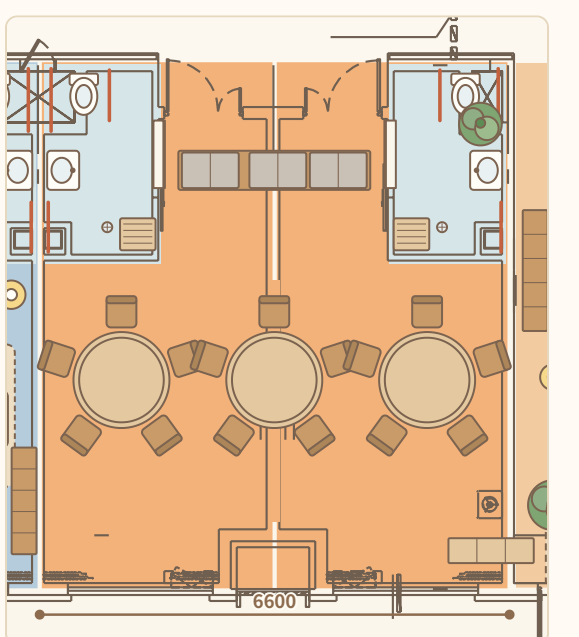

- 圆桌 6 人 × 3 = 18 座，圈椅带扶手，桌下净高 ≥ 700
- 助餐台 + 保温柜 + 洗消，热食备餐间紧邻
- 餐时错峰 · 助餐员一对一服务

4 多功能活动厅群

ACTIVITY WING

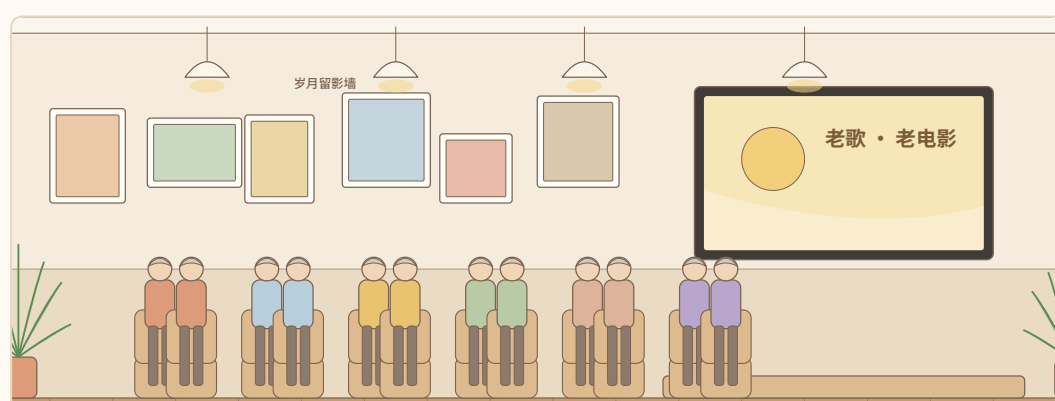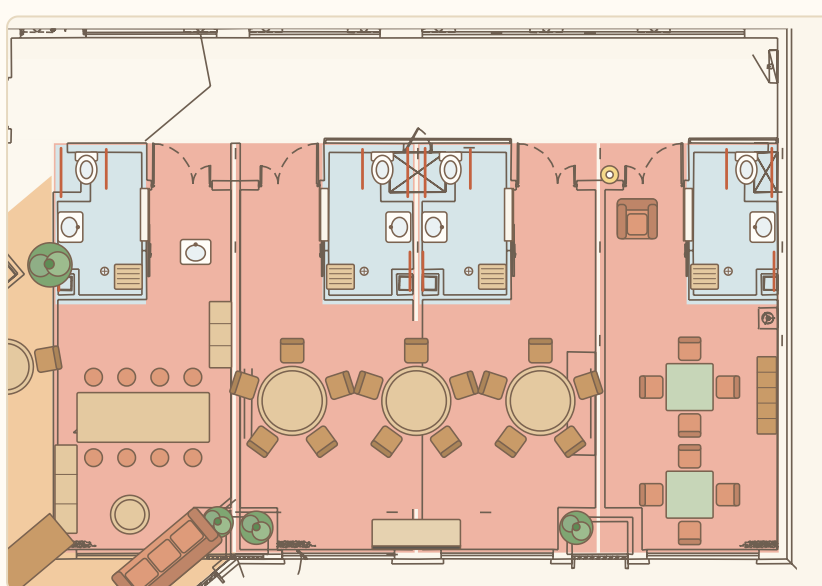

- 书画手工 / 怀旧影院 / 棋牌阅览三室连片，可整体打开
- 转角翼 40° 斜向，形成有变化的“街角”感
- 暖黄灯光 + 岁月留影墙，唤起共同记忆

5 面积表

SCHEDULE · ㎡

功能用房	㎡	服务 · 交通	㎡
01 值班 · 安防	23.6	医用电梯	5.6
02 健康小屋 · 医务	23.6	楼梯	17.0
03 康复训练室	47.2	电梯 × 2	8.1
04 中医理疗室	23.6	楼梯	12.5
05 心理 · 谈话室	23.6	无障碍厕所	3.5
06 长者食堂 · 助餐	47.2	公共卫生间	9.3
07 门厅 · 接待 · 茶座	43.9	更衣 · 库房	6.8
08 书画 · 手工坊	23.6	办公 · 社工站	10.9
09 多功能活动厅	47.2	热食备餐间	10.1
10 棋牌 · 阅览	23.6	无障碍卫生间	4.5
		安防 · 消控	11.6

医护 · 健康 71㎡ · 22% 康复 · 理疗 71㎡ · 22% 餐饮 · 备餐 47㎡ · 14% 接待 · 门厅 44㎡ · 13% 文娱 · 活动 94㎡ · 29% 面积为按图纸推算的净面积约数（含居室内卫生间）。

6 节点详图

DETAILS

