

二层 · 居住照护层

12 间朝南居室 · 日光起居厅 · 护理站 · 助浴
回到家，回到自己的房间

本层功能

12

间单人居室

23.6

m²/间

43.9

m² 日光起居厅


PROGRAMME

1.8

m 中廊

居室 (=居住单元): 入口前室 + 卫生间 + 3.3×4.6m 起居卧室; 东端日光厅承担全屋“客厅 + 餐厅”。

电梯直达 护理站居中 助浴间 记忆走廊 转角翼

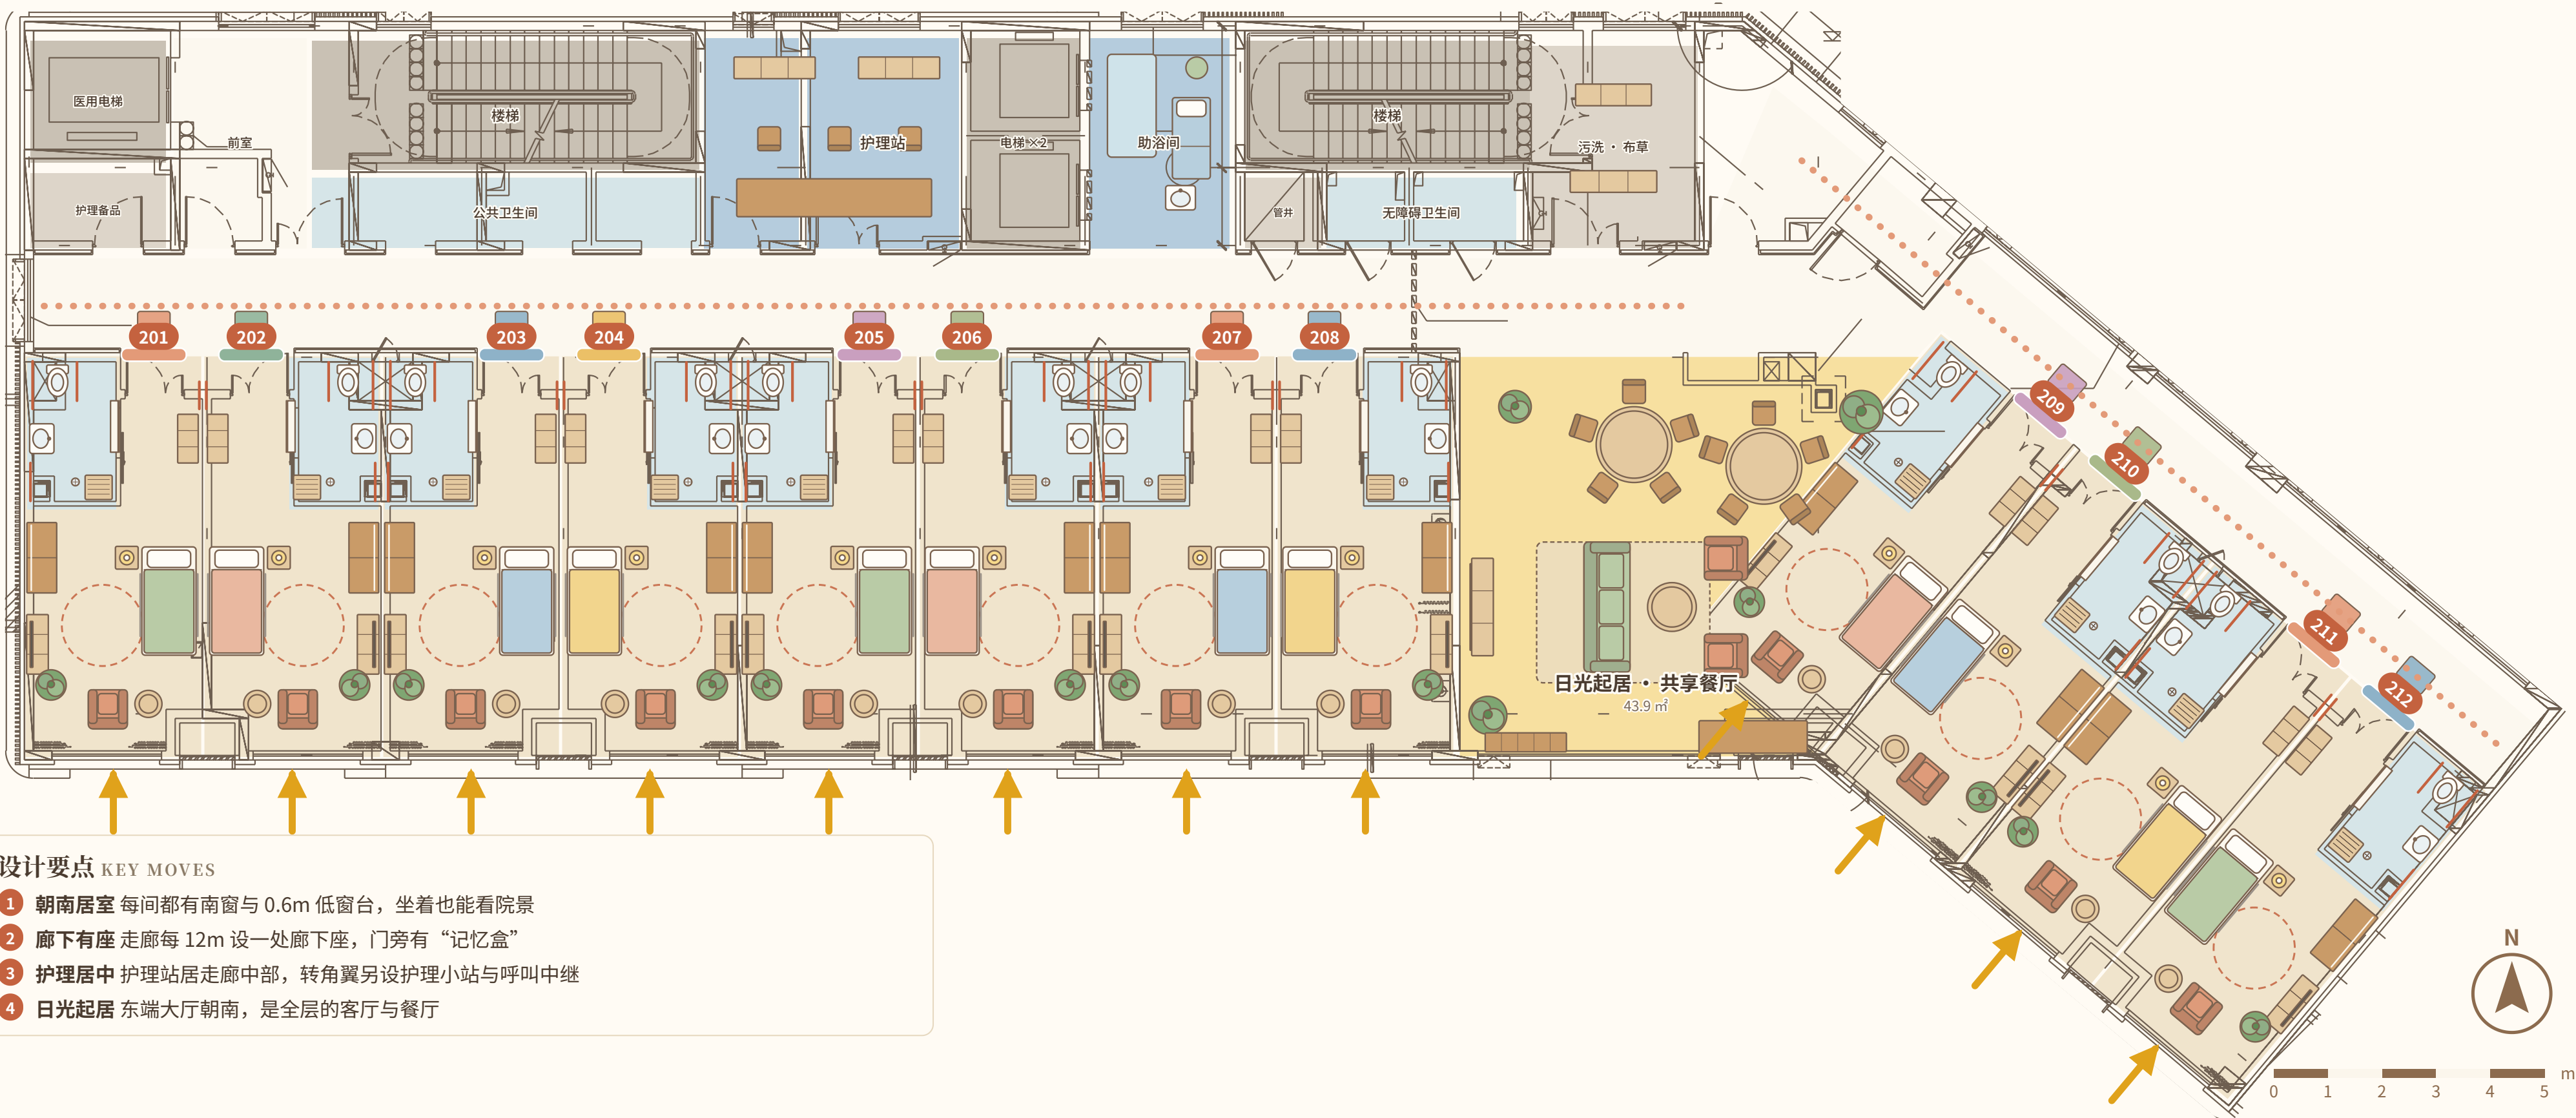

设计要点 KEY MOVES

- 1 朝南居室 每间都有南向与 0.6m 低窗台，坐着也能看院景
- 2 廊下有座 走廊每 12m 设一处廊下座，门旁有“记忆盒”
- 3 护理居中 护理站居走廊中部，转角翼另设护理小站与呼叫中继
- 4 日光起居 东端大厅朝南，是全层的客厅与餐厅

二层平面图 SECOND FLOOR PLAN 1: 90 (示意，随排版比例) · 黄色箭头: 南向自然光


A 寻路与记忆

WAYFINDING




B 护理与疏散

CARE ROUNDS

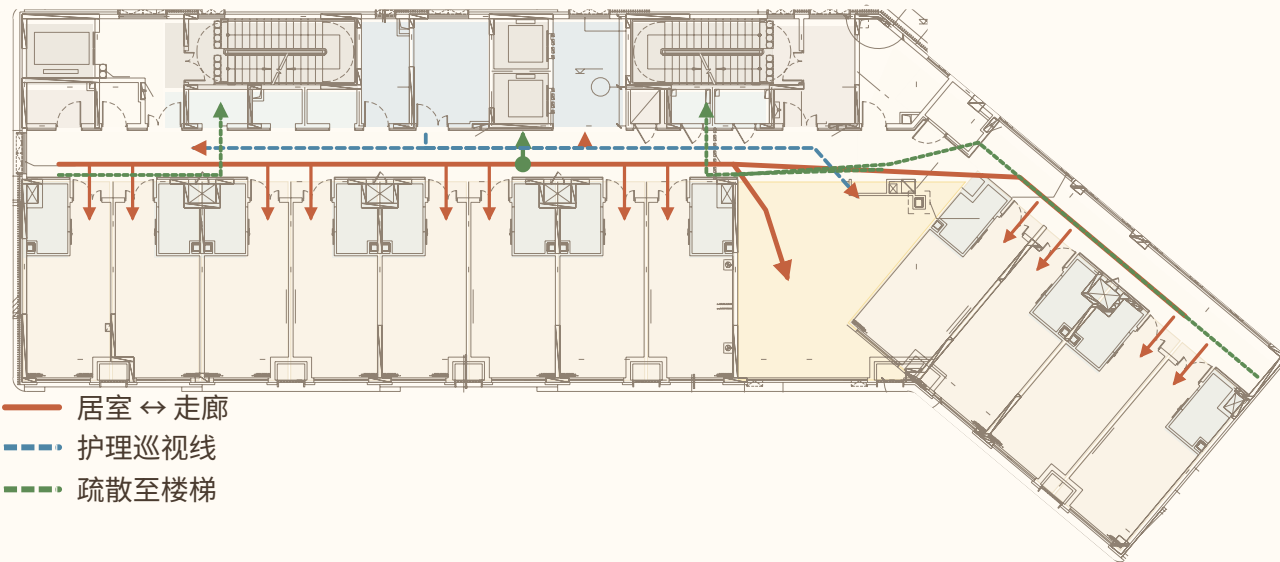


C 安全与呼叫

SAFETY

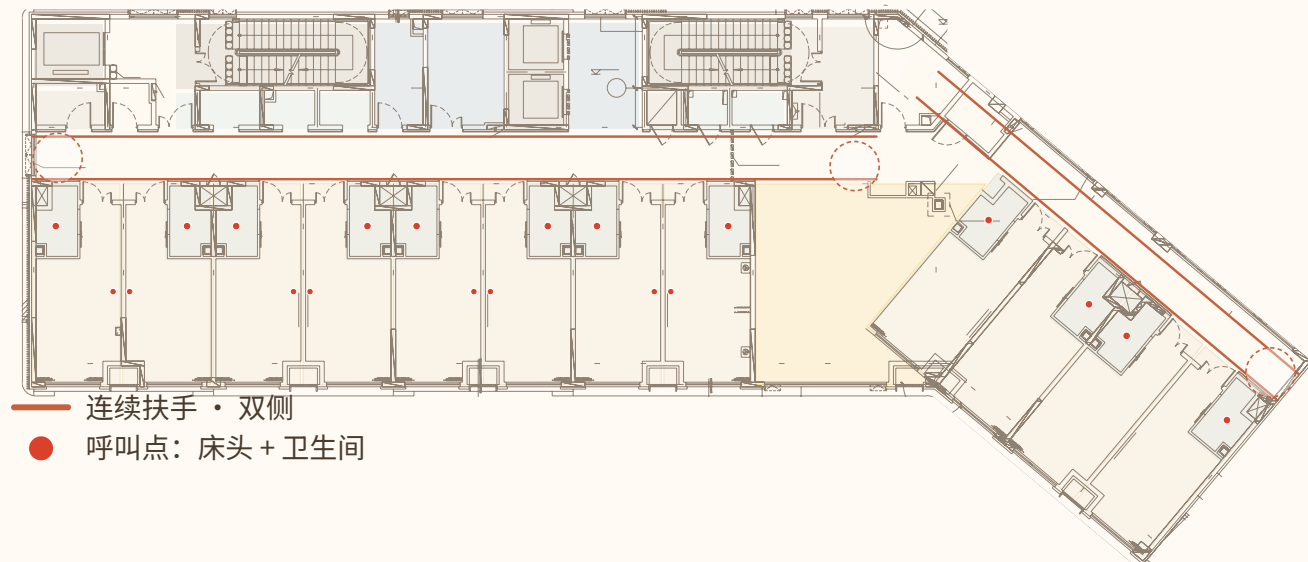

1 标准居室 (镜像成对)


TYPICAL ROOM · 23.6m²

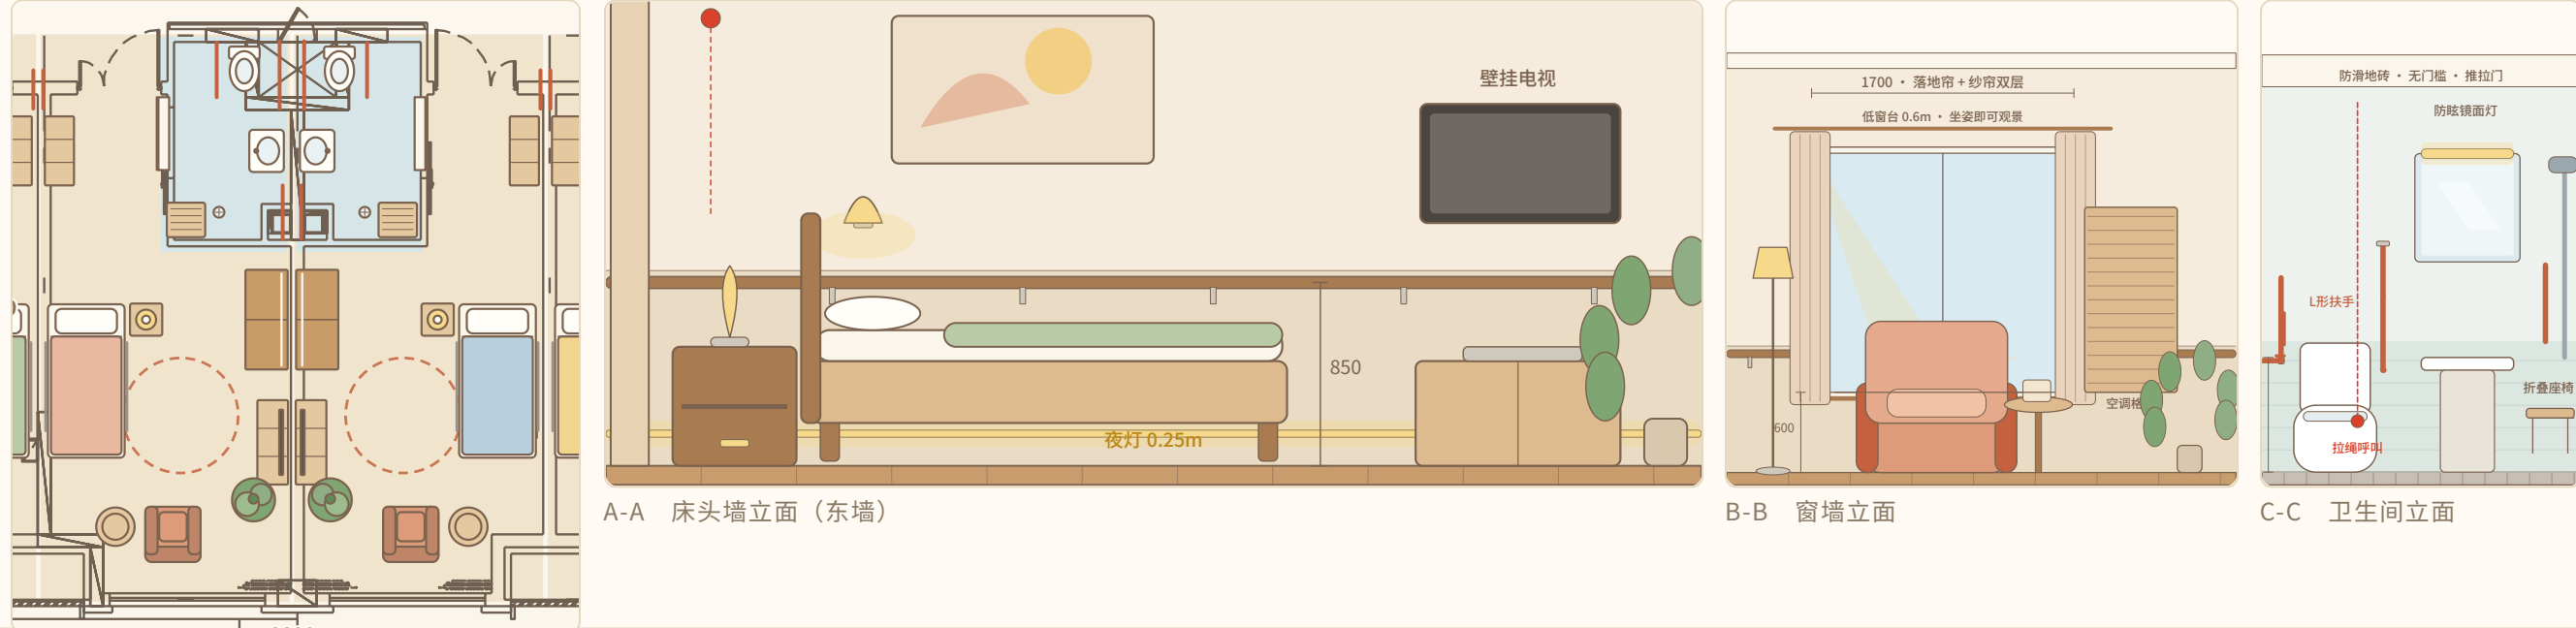

- 床: 电动护理床 1000×2000, 床头靠实墙, 一侧留 ≥1200 供轮椅转移
- 床头: 壁灯 + 拉绳呼叫 + 夜灯; 床头柜圆角、抽屉带扶把
- 床→卫生间: 脚灯 (0.25m) 连通, 推拉门零门槛, 路径 ≤3m
- 卫生间 1.7×2.9m: 折叠淋浴座椅、L 形 + 竖向扶手、地漏中置、防眩镜灯
- 窗前: 低窗台 0.6m + 扶手椅 + 边几, 是老人“看世界”的位置
- 收纳: 衣柜推拉门, 把手在 0.9–1.1m; 上层放不常用物品

2 日光起居 · 共享餐厅

SUNLIT LIVING & DINING

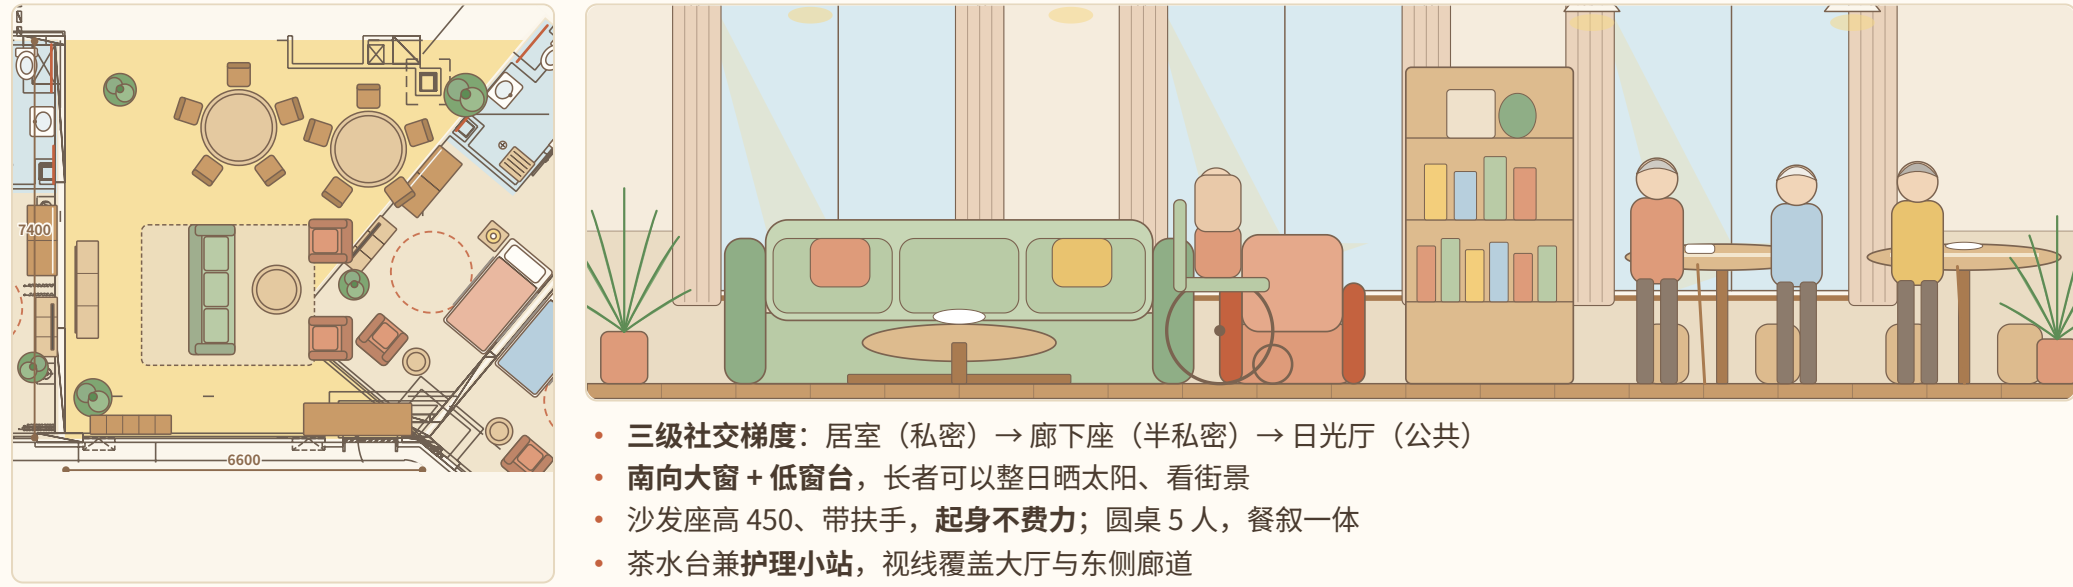

- 三级社交梯度: 居室 (私密) → 廊下座 (半私密) → 日光厅 (公共)
- 南向大窗 + 低窗台, 长者可以整日晒太阳、看街景
- 沙发座高 450、带扶手, 起身不费力; 圆桌 5 人, 餐叙一体
- 茶水台兼护理小站, 视线覆盖大厅与东侧廊道

3 护理站 · 助浴间

NURSING & ASSISTED BATH



- 护理站居走廊中部, 双层台面 750 / 1100, 坐立皆宜
- 助浴间: 升降浴床 + 淋浴椅, 地面防滑排水, 室温 ≥26°C
- 药品耗材嵌入柜体; 呼叫看板实时显示各房间状态

4 记忆走廊

MEMORY CORRIDOR



- 色彩记忆条: 门楣 6 色循环, 眼高位置, 记住颜色即记住房间
- 记忆盒: 门旁壁龛, 放老照片与小物件, 自带识别与话题
- 视觉地标: 走廊端景为窗 / 绿植 / 挂画, 形成路径节点
- 廊下座: 每 ≤12m 一处, 扶手连续, 可歇脚聊天
- 地面: 无反光哑光地胶, 避免暗色块 (易被误认为台阶)


5 居室家具设备清单

FURNITURE · PER ROOM

名称	规格 mm	数量	备注
电动护理床	1000×2000×500 可调	1	带护栏 · 呼叫器
床头柜	450×450×550	1	圆角 · 夜灯
衣柜 (推拉门)	1300×550×2000	1	把手 0.9–1.1m
高座扶手椅	720×720×900	1	座高 450
圆边几	Ø500×500	1	软包边
电视柜 + 电视	1100×400	1	壁挂 · 遥控
落地灯 (暖光)	Ø300×1500	1	3000K
折叠淋浴座椅	450×450	1	座高 450
L 形 / 竖向扶手	Ø40	3–4	卫生间 · 床边
呼叫器 + 拉绳	床头 + 卫生间	2	双回路 · 应急
床头壁灯 (阅读)	Ø120 · 可调	1	3000K 防眩
防滑地垫 / 地毯	1600×2300	1	低绒 · 防边翘
记忆盒 (门旁)	300×350×120	1	壁龛 · 可换

6 转角翼 · 认知友好

CORNER WING

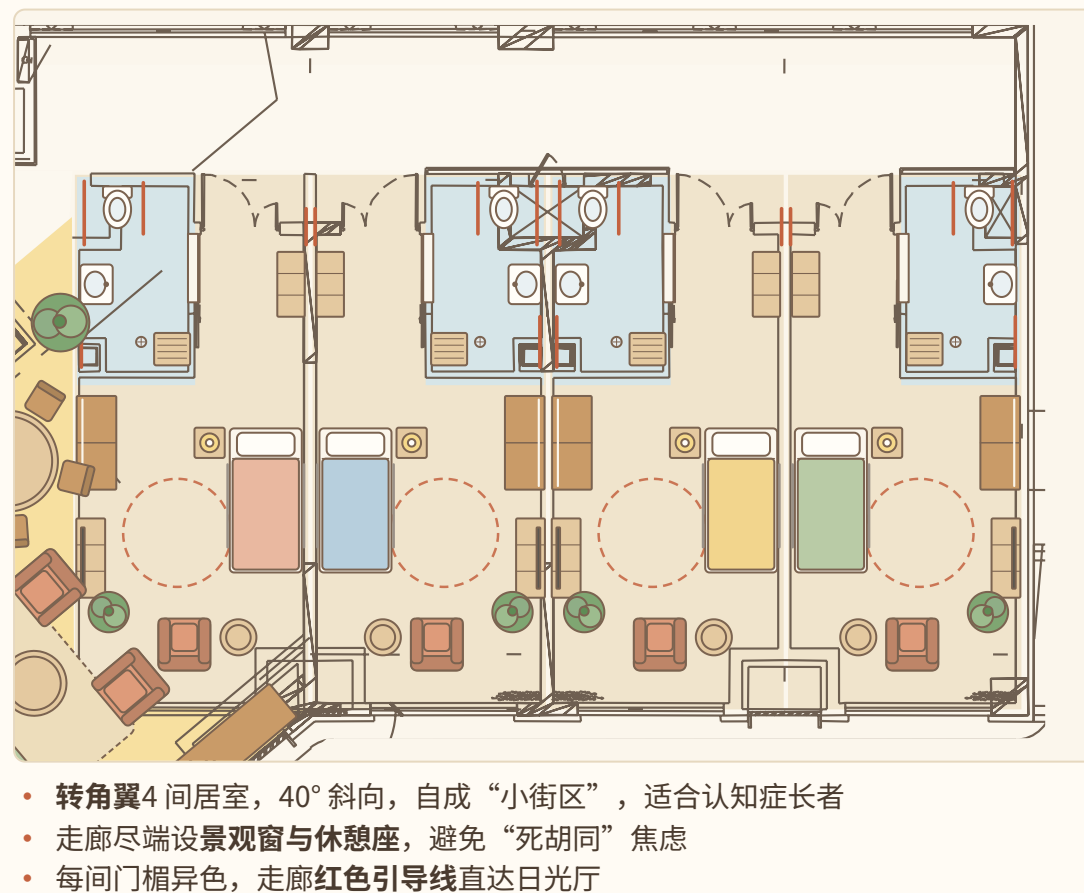

- 转角翼 4 间居室, 40° 斜向, 自成“小街区”, 适合认知症长者
- 走廊尽端设景观窗与休憩座, 避免“死胡同”焦虑
- 每间门楣异色, 走廊红色引导线直达日光厅