

暖阳颐养之家

社区嵌入式养老服务中心 · 室内设计方案

WARM SUN CARE HOME — an age-friendly interior for a two-storey community centre

让老去，被温柔地接住




二层·居住照护层 FIRST-PERSON AERIAL · UPPER FLOOR

整层朝南



日光起居·共享餐厅 SUNLIT LIVING & DINING

全天有光

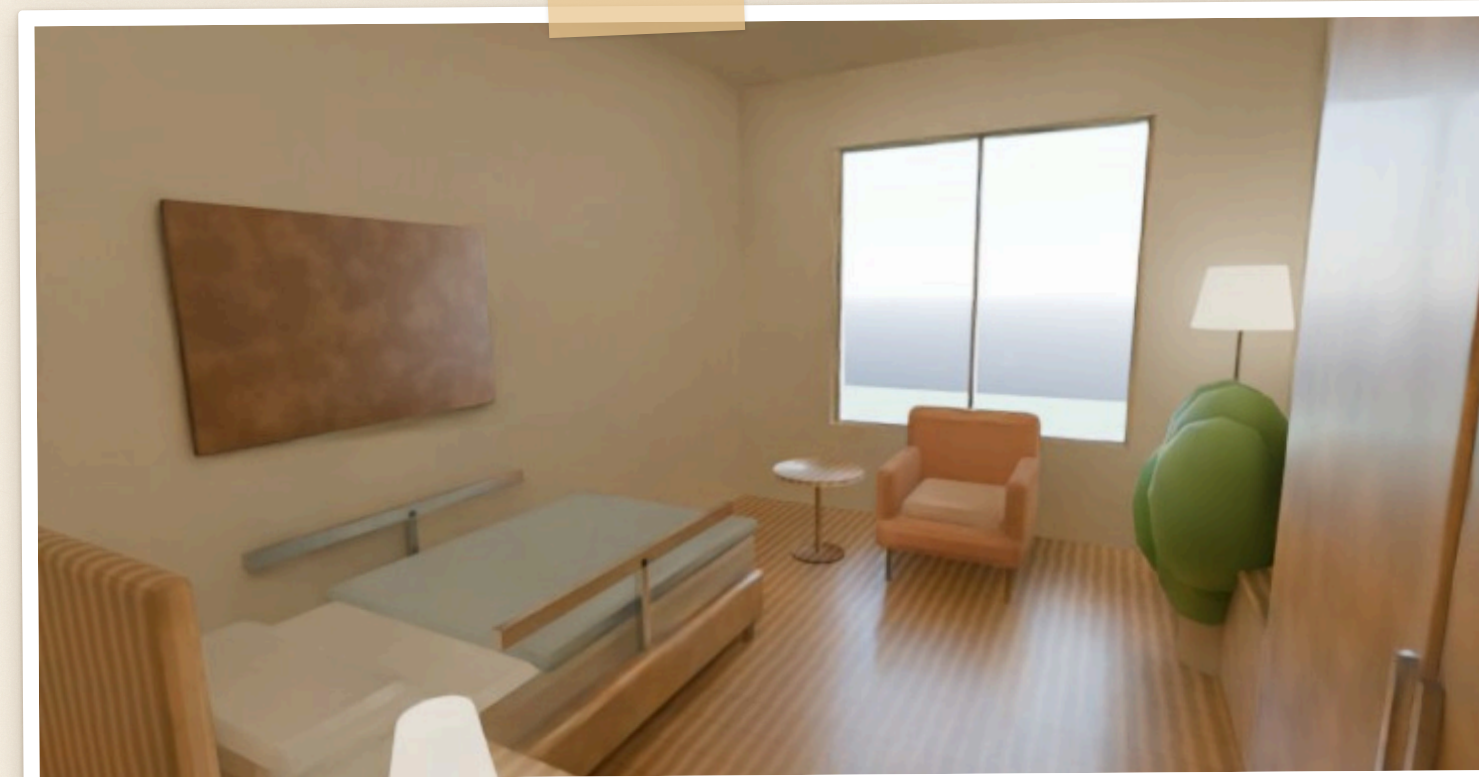


标准居室 TYPICAL ROOM

我的小家




门厅·接待·茶座 LOBBY & TEA LOUNGE

进门就暖

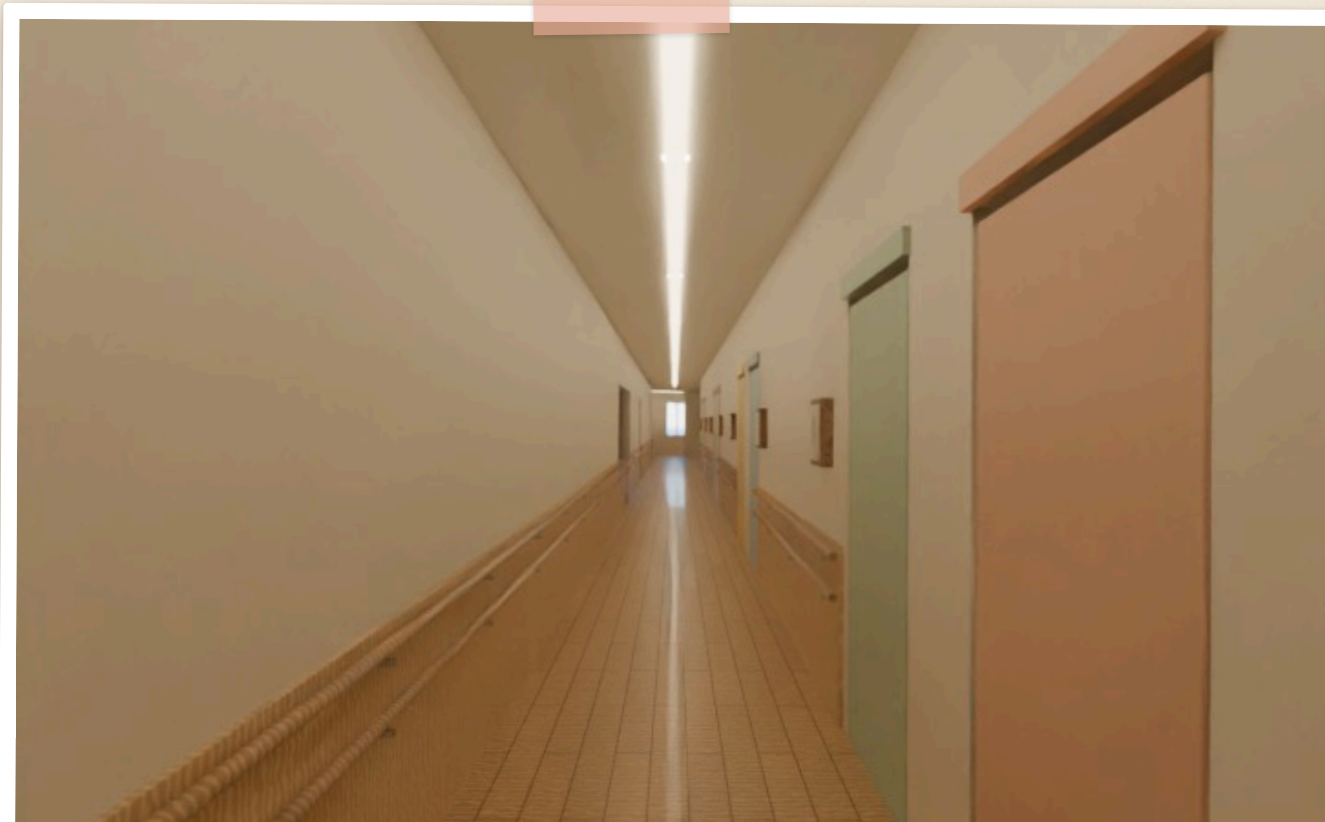

记忆走廊 MEMORY CORRIDOR

认得出自己的门

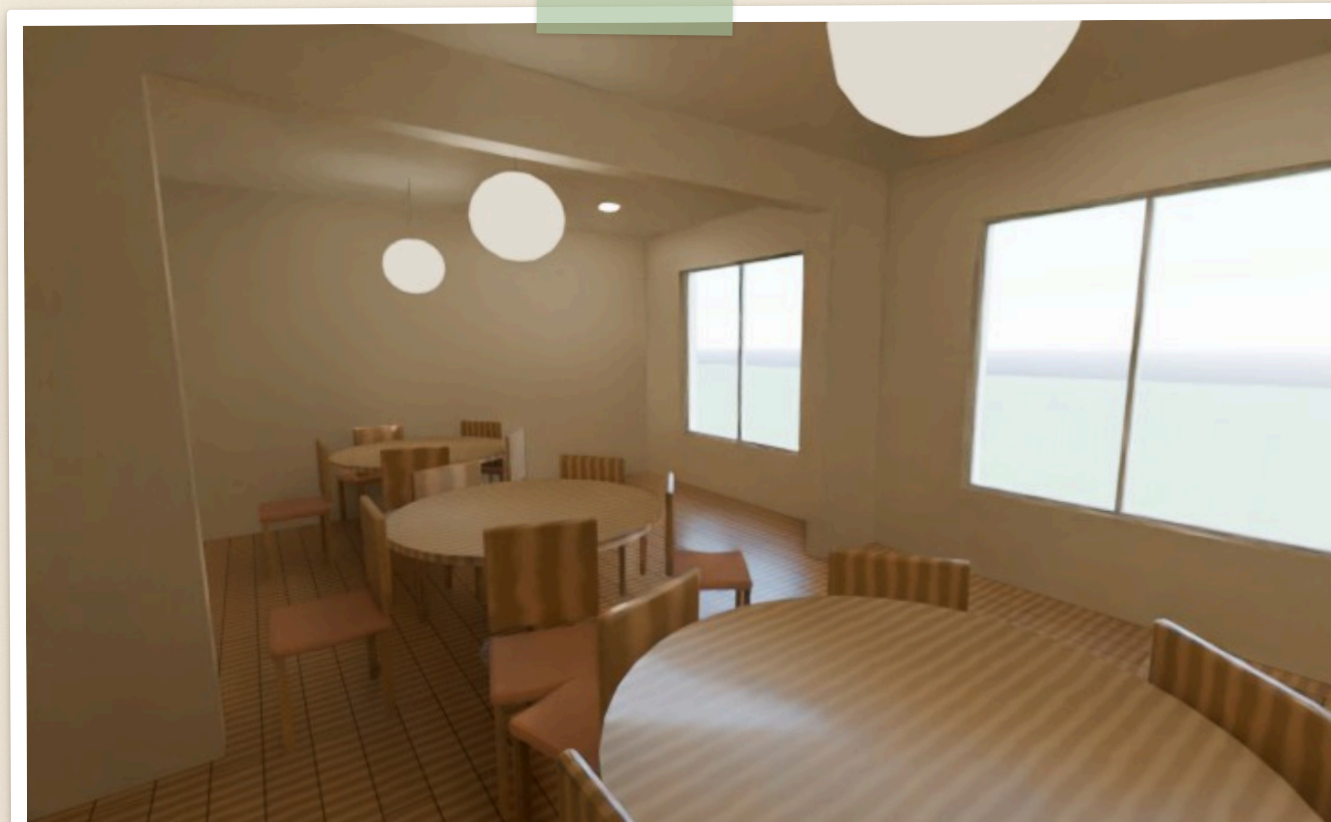

长者食堂·助餐 COMMUNITY CANTEEN

热乎的一顿饭

01 设计理念

CONCEPT

图纸是一栋规整的两层楼：南侧 8 间 3.3m 开间单元、1.8m 中廊，东端 6.6m 大厅，再折出 4 间 40° 转角翼。

化整为零 一个开间即一间居室，保持“家”的尺度。

阳光向南 居室与日光厅朝南，整日有光。

公共在下，私密在上 一层接纳社区与康复，二层留给睡眠与陪伴。

去机构化 医疗设备隐入柜体，以织物、灯具营造居家氛围。

02 适老五原则

FIVE PRINCIPLES

- 安 SAFE**
走廊净宽约1.8m，双层连续扶手，无门槛、防滑地胶、家具全圆角
- 暖 WARM**
暖木·奶油白·陶土·鼠尾草绿；触感柔软，避免冷金属与强反光
- 明 BRIGHT**
南向自然光+3000K暖白光；低眩光，夜间0.25m 脚灯
- 忆 MEMORY**
门框色彩记忆条、“记忆盒”、廊内视觉地标，降低迷路焦虑
- 伴 TOGETHER**
居室—廊下座—日光厅/食堂，三级社交梯度

03 色彩与氛围


COLOUR & MOOD



暖色亲近，雾蓝静谧；晨光黄与陶土作视觉地标。

04 功能分区


FUNCTION ZONING

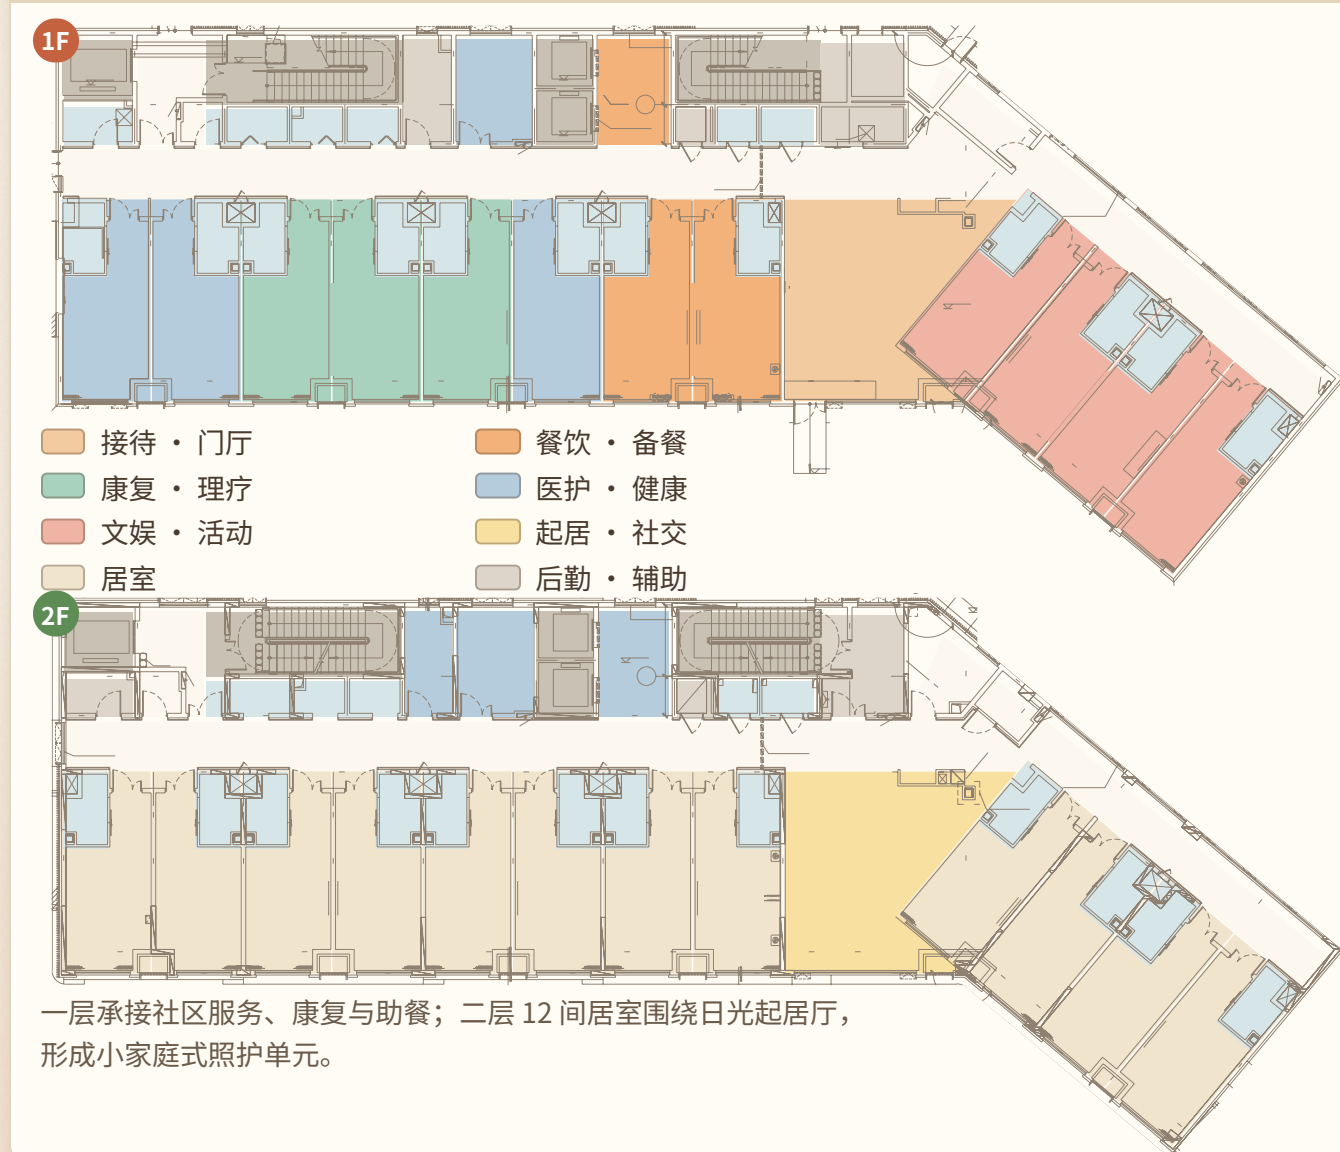

一层承接社区服务、康复与助餐；二层 12 间居室围绕日光起居厅，形成小家庭式照护单元。

05 动线分析


CIRCULATION

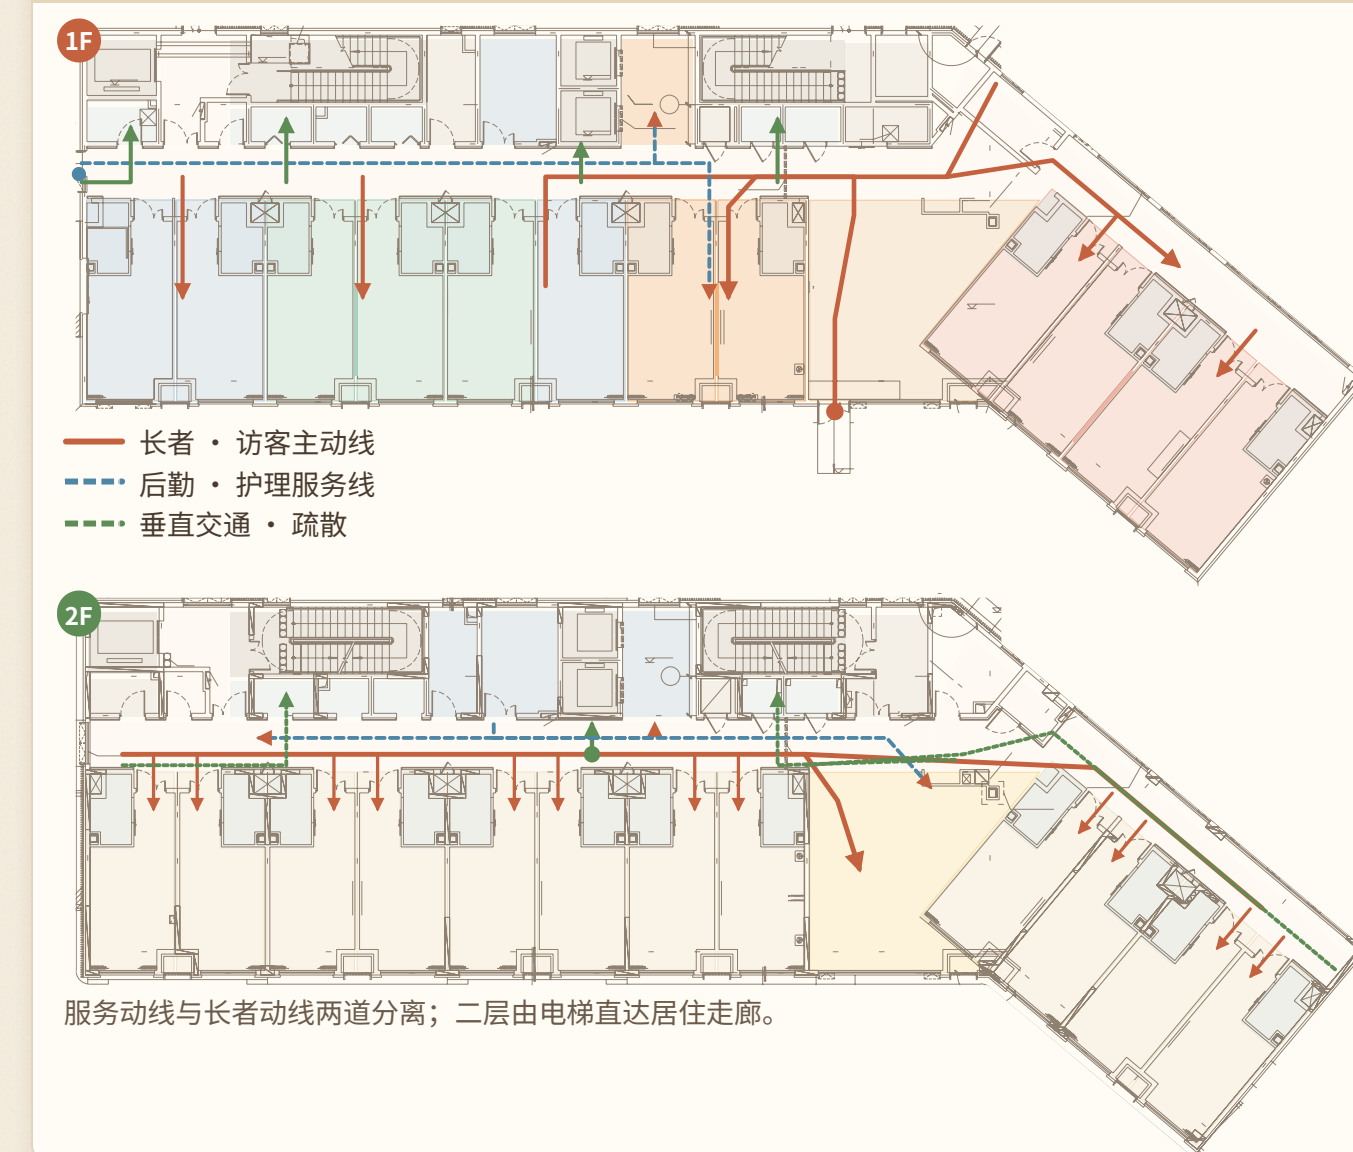

服务动线与长者动线两道分离；二层由电梯直达居住走廊。

06 光环境


LIGHT

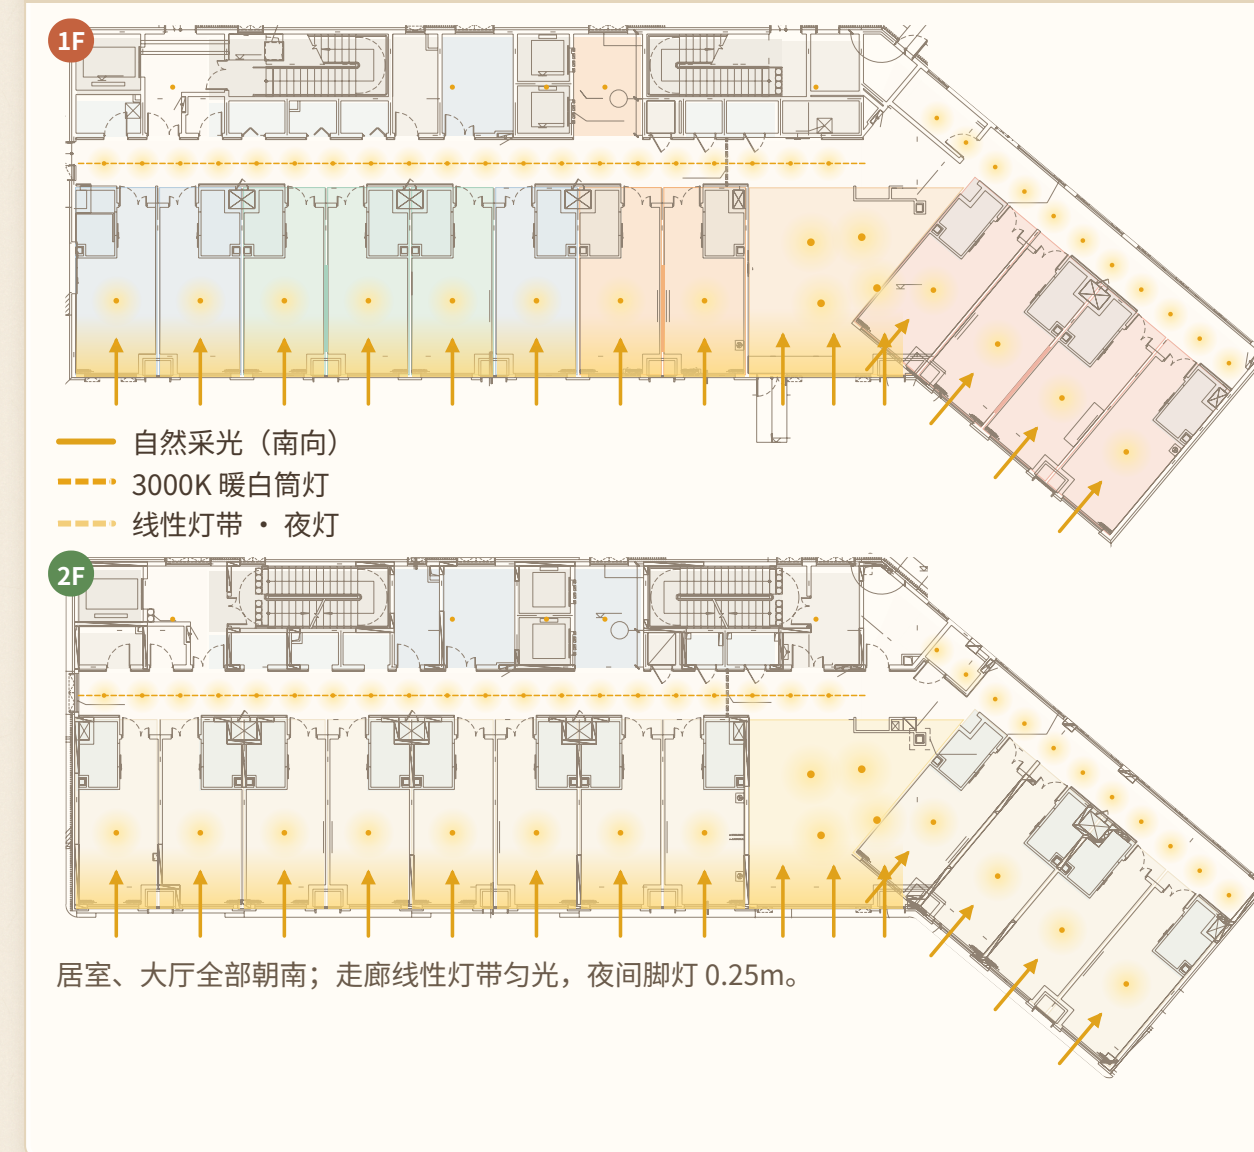

居室、大厅全部朝南；走廊线性灯带匀光，夜间脚灯 0.25m。

07 材质板

MATERIAL BOARD

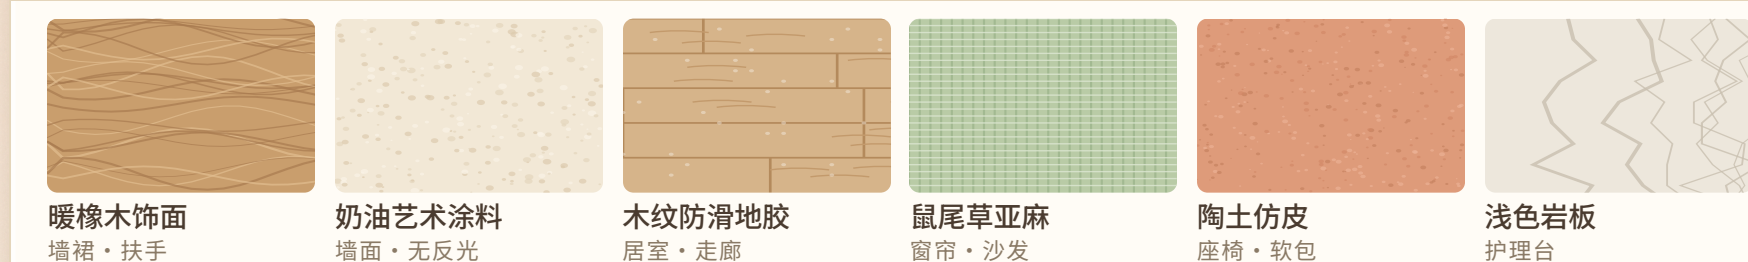

08 适老关键尺度

DIMENSIONS · MM

走廊净宽	≥ 1800	约1.8m
居室门净宽	1000	含推拉门
连续扶手	650 / 850	双层
护理床面高	500	可调
轮椅回转	Ø1500	居室·卫生间
坐姿窗台	≤ 600	低窗台

09 项目指标

KEY FIGURES

2 层	12 间单人居室	≈ 1160 m ² 总建筑面积
≈ 23.6 m ² /间 (含卫)	1.8 m 走廊净宽	3.3 m 居室开间