


二层 · 居住照护层

12 间朝南居室 · 日光起居厅 · 护理站 · 助浴

回到家，回到自己的房间

二层平面图 SECOND FLOOR PLAN

1:90 · 示意 · 黄色箭头为南向自然光

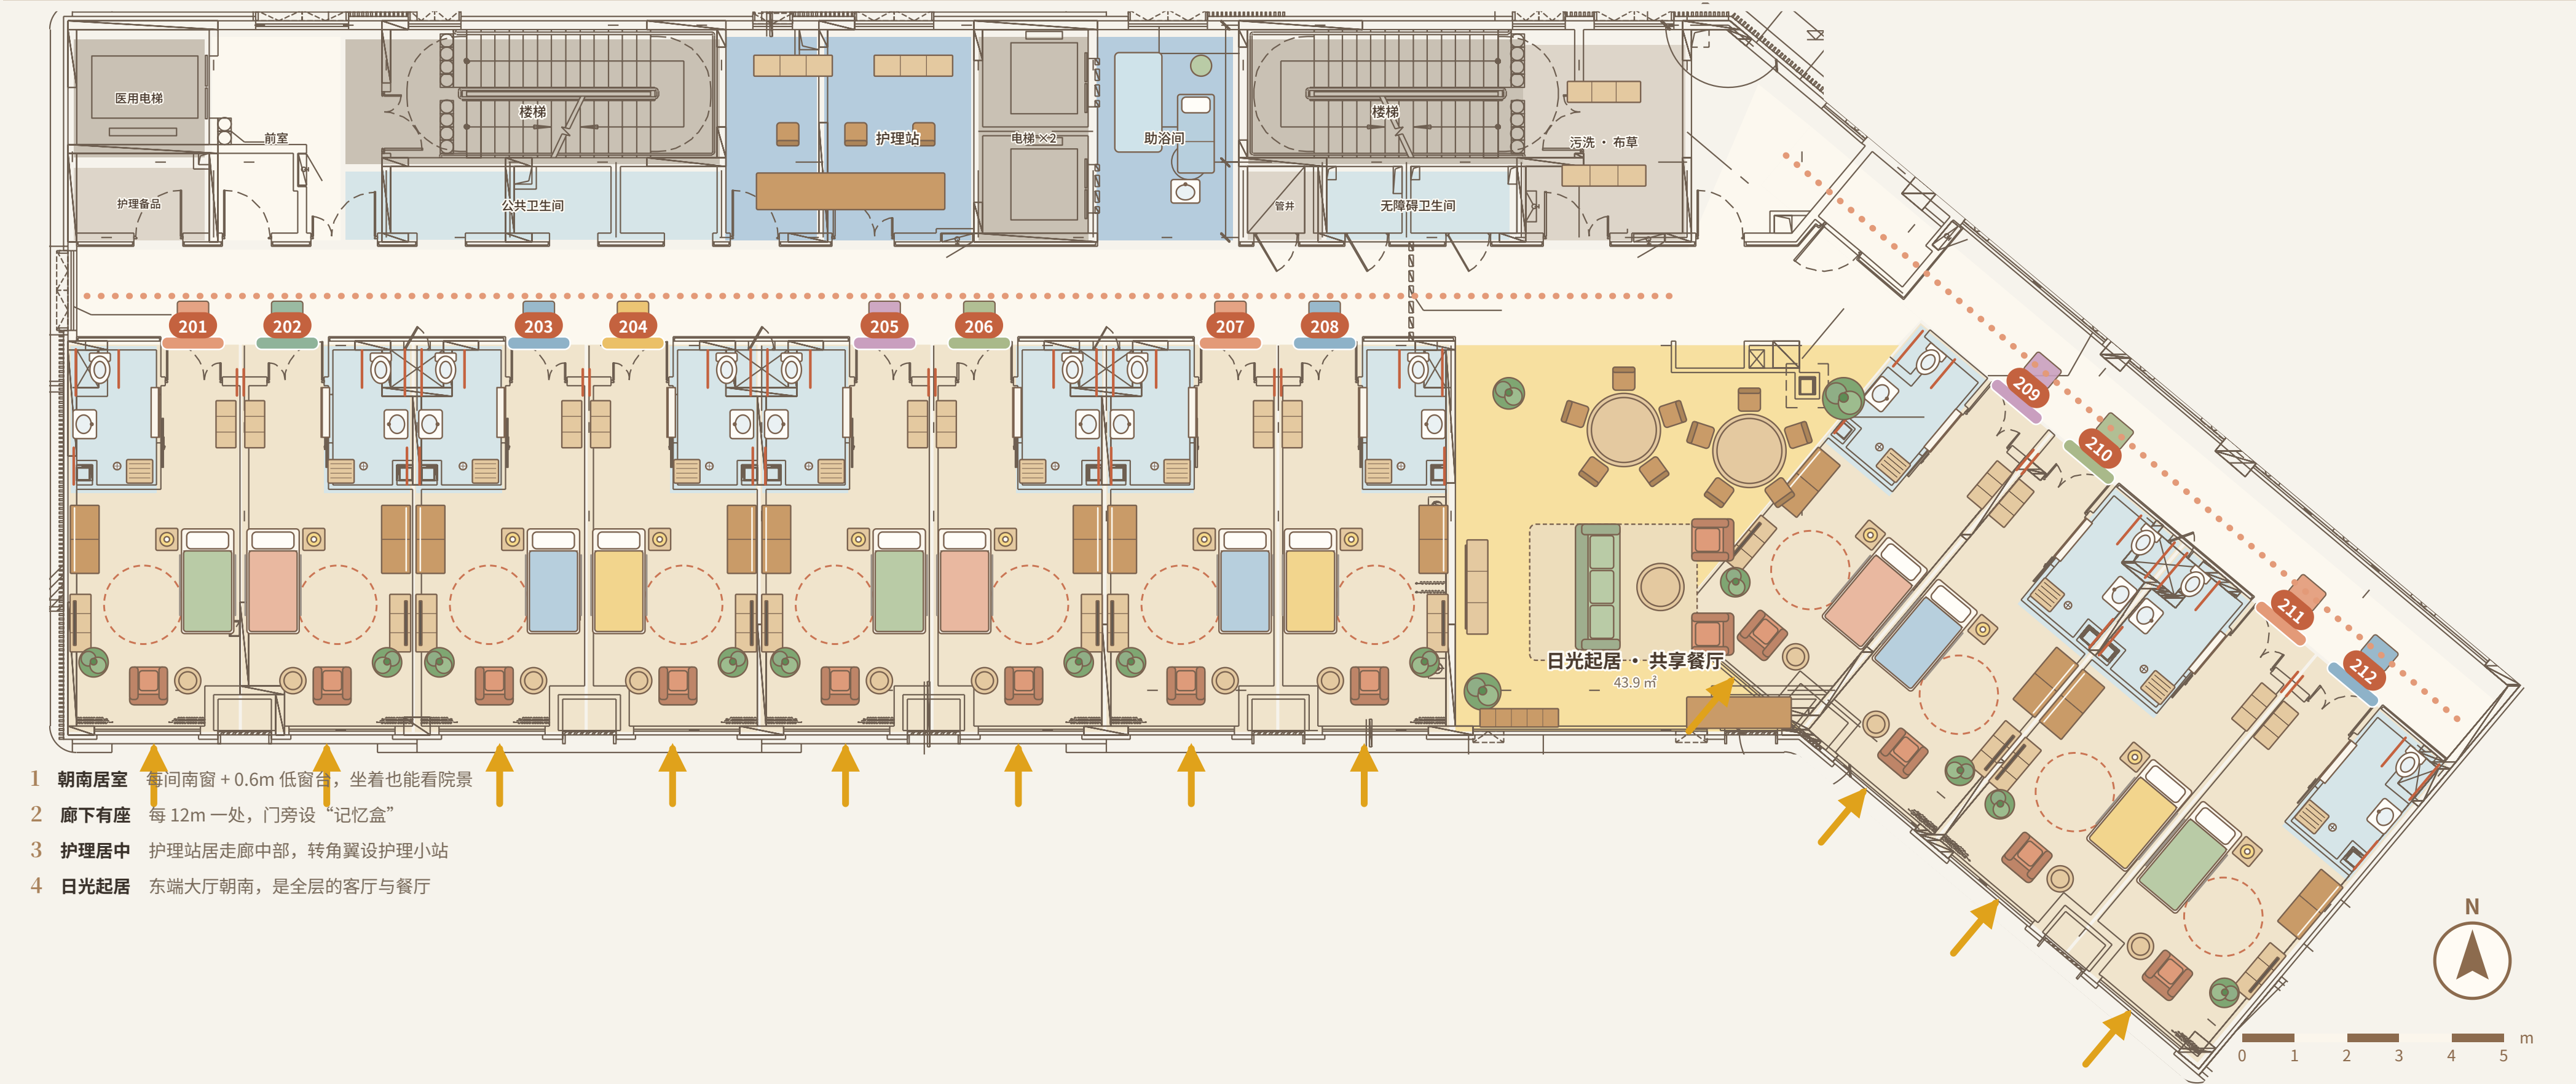


策略分析 DESIGN ANALYSIS

寻路与记忆 WAYFINDING




— 门楣色彩记忆条 — 色彩引导线

护理与疏散 CARE ROUNDS

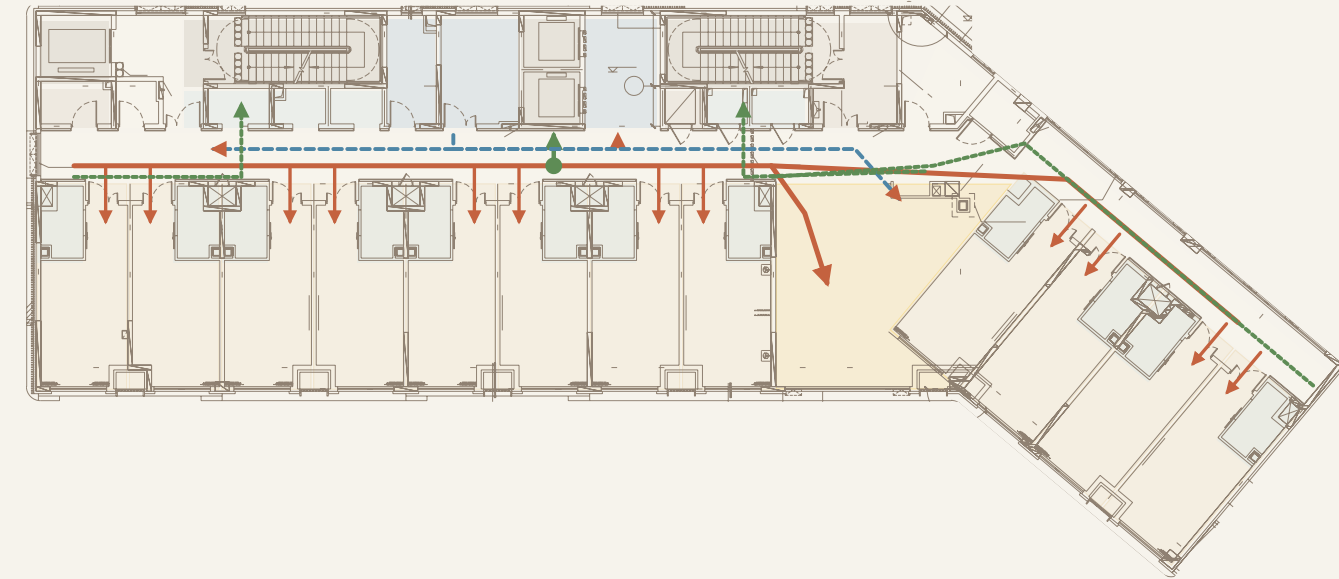


— 居室 ↔ 走廊 — 护理巡视 - - - 疏散

安全与呼叫 SAFETY

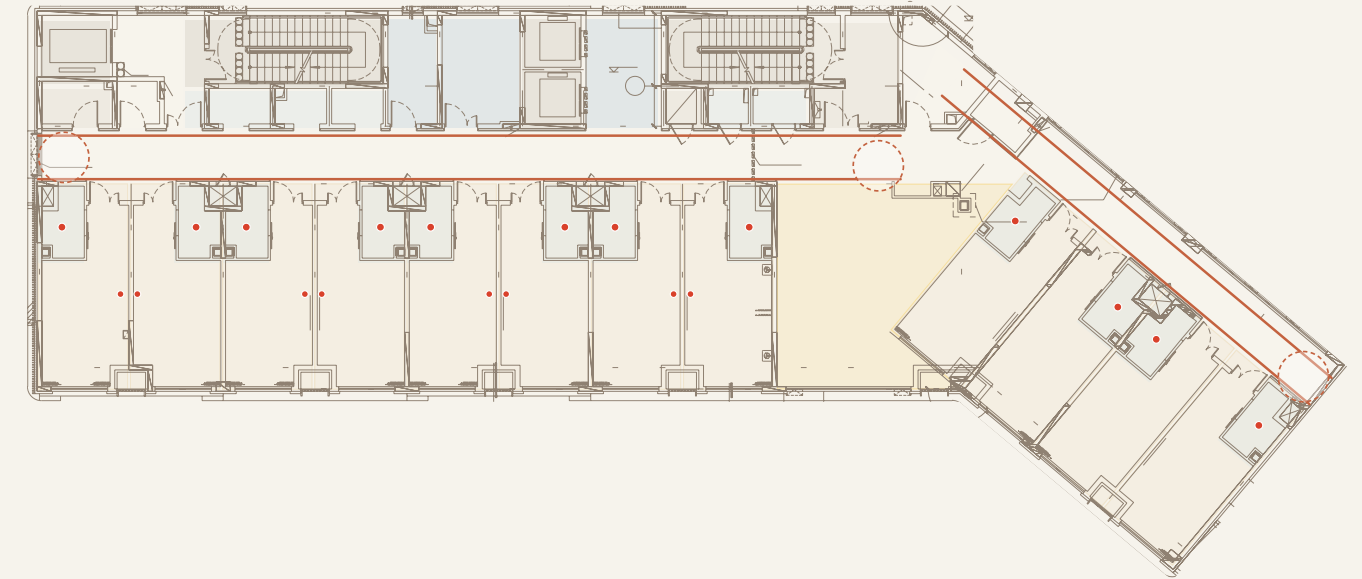

— 双侧扶手 ● 呼叫：床头 + 卫生间

重点空间 KEY SPACES

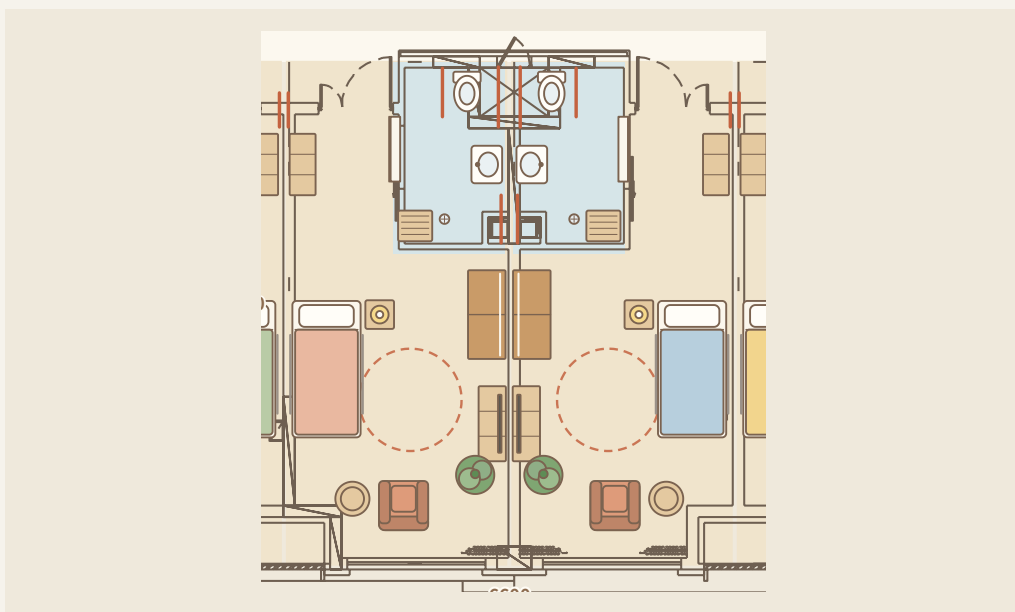


标准居室平面 TYPICAL ROOM 23.6㎡

床边留 ≥1200 供轮椅转移；床→卫生间 ≤3m，脚灯连通。




日光起居 · 共享餐厅 LIVING & DINING

居室 → 廊下 → 日光厅，三级社交

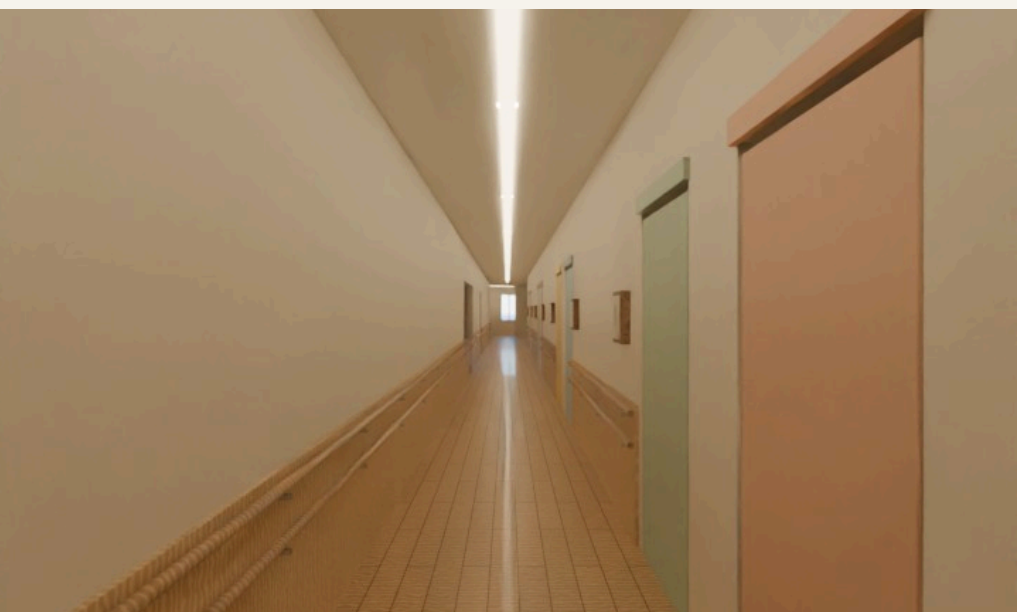

记忆走廊 CORRIDOR

门楣色彩 + 记忆盒，认得出自己的门

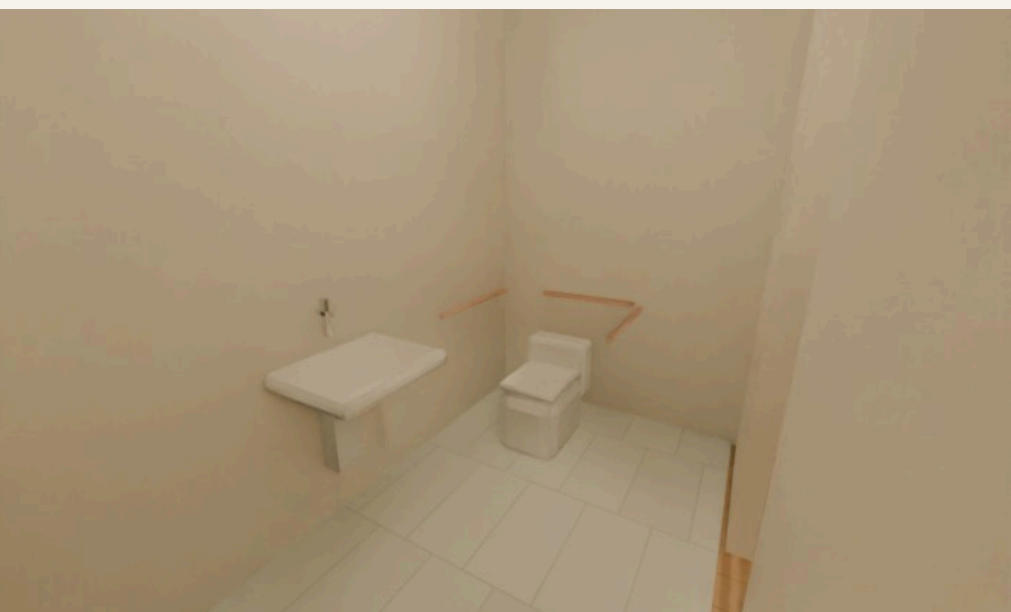

无障碍卫生间 ACCESSIBLE BATH


L形扶手、折叠座椅、零门槛推拉门

居室家具清单 FURNITURE · PER ROOM

电动护理床	1000×2000×500	带护栏 · 呼叫器	落地灯	Ø300×1500	3000K
床头柜	450×450×550	圆角 · 夜灯	折叠淋浴座椅	450×450	座高 450
衣柜 (推拉门)	1300×550×2000	把手 0.9-1.1m	L 形 / 竖向扶手	Ø40	3-4 根
高座扶手椅	720×720×900	座高 450	呼叫器 + 拉绳	床头 + 卫生间	双回路
圆边几	Ø500×500	软包边	床头壁灯	Ø120	3000K 防眩
电视柜 + 电视	1100×400	壁挂	记忆盒 (门旁)	300×350×120	壁龛 · 可换

四色被面对应四种门楣色；床头墙立面与窗前扶手椅，是老人“看世界”的位置。

走廊墙面 CORRIDOR ELEVATION

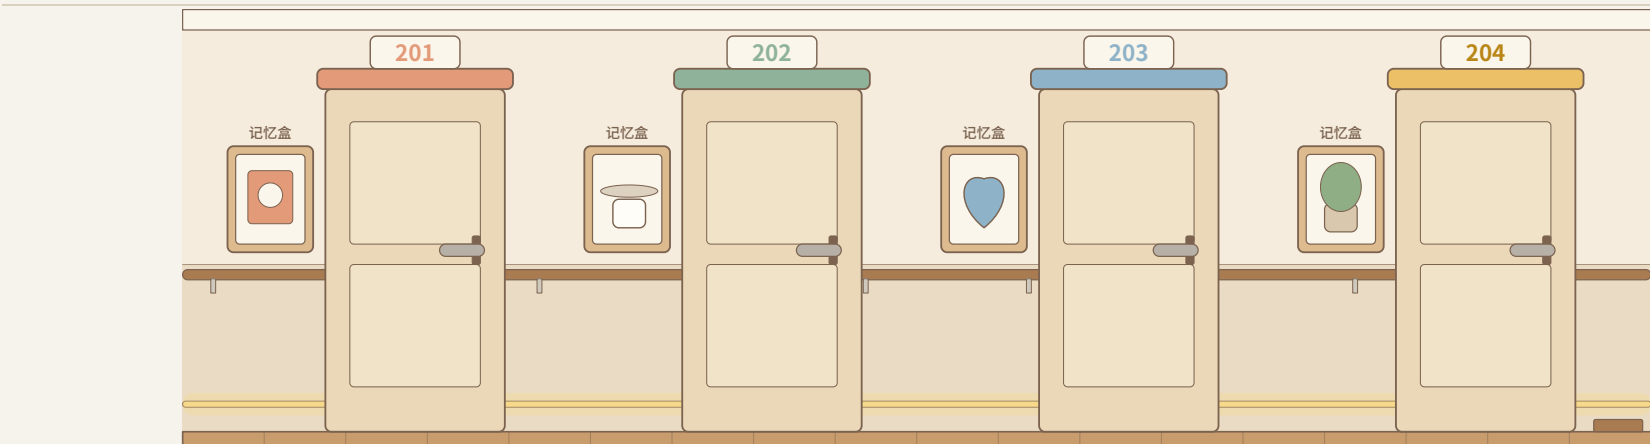

走廊净宽约 1.8m，双侧连续扶手 650 / 850；地面哑光，避免暗色块（易被误认为台阶）；走廊端景为窗 / 绿植。