

暖阳颐养之家

社区嵌入式养老服务中心 室内设计方案

让老去，被温柔地接住
WARM SUN CARE HOME

设计理念 CONCEPT

温

WARM

暖木、奶油白、陶土与鼠尾草绿，触感柔软

安

SAFE

无门槛、双层扶手、防滑地胶、全圆角

明

BRIGHT

南向日光与 3000K 暖白光，夜间脚灯

忆

MEMORY

色彩门框、记忆盒、走廊视觉地标

伴

TOGETHER

居室 → 廊下座 → 日光厅，三级社交


像家一样熟悉，比家更安心

空间总览 EXPLODED AXONOMETRIC

一层公共服务 · 二层居住照护



1 门厅·接待 2 长者食堂 3 康复训练 4 医务·值班 5 多功能活动厅 6 日光起居·共享餐厅 7 居室×8 8 转角翼居室×4 9 护理站

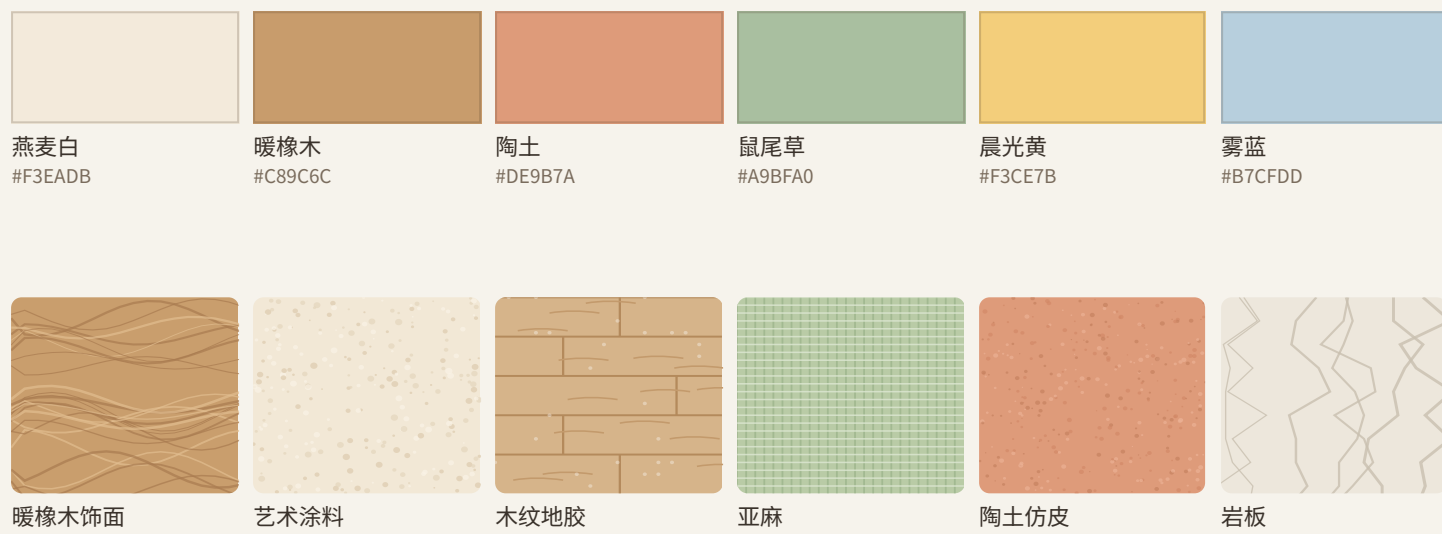

材质原则 哑光、无反光、抗菌易清洁；边角一律圆角收边，触感温润。

2 层 12 间居室 ≈1160 m² 建筑面积 1.8 m 走廊净宽

面积按图纸推算 (1pt=0.1m)，为约数；JGJ 450 / GB 50763 作参考，数值待深化复核。

空间意象 SPACE IMPRESSIONS



居室 ROOM



记忆走廊 CORRIDOR



长者食堂 CANTEEN



门厅·茶座 LOBBY

策略分析 DESIGN ANALYSIS


一层 / 二层

功能分区 ZONING




接待·门厅 餐饮·备餐 康复·理疗 医护·健康 文娱·活动 起居·社交

动线 CIRCULATION

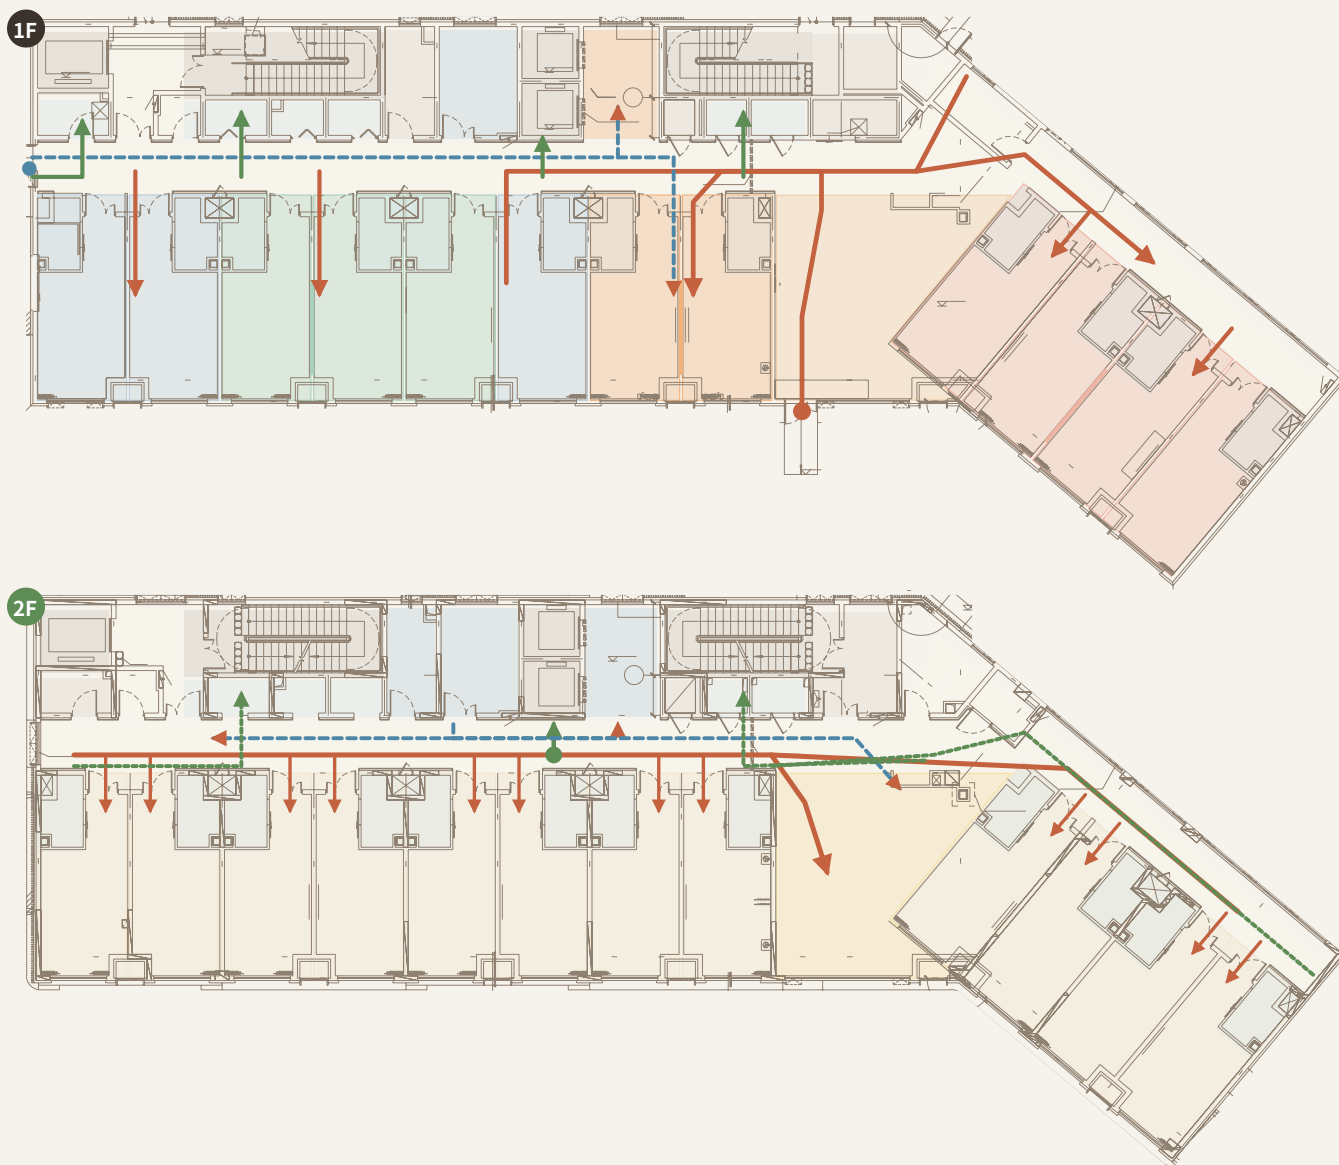

长者动线 服务动线 疏散

光环境 LIGHT

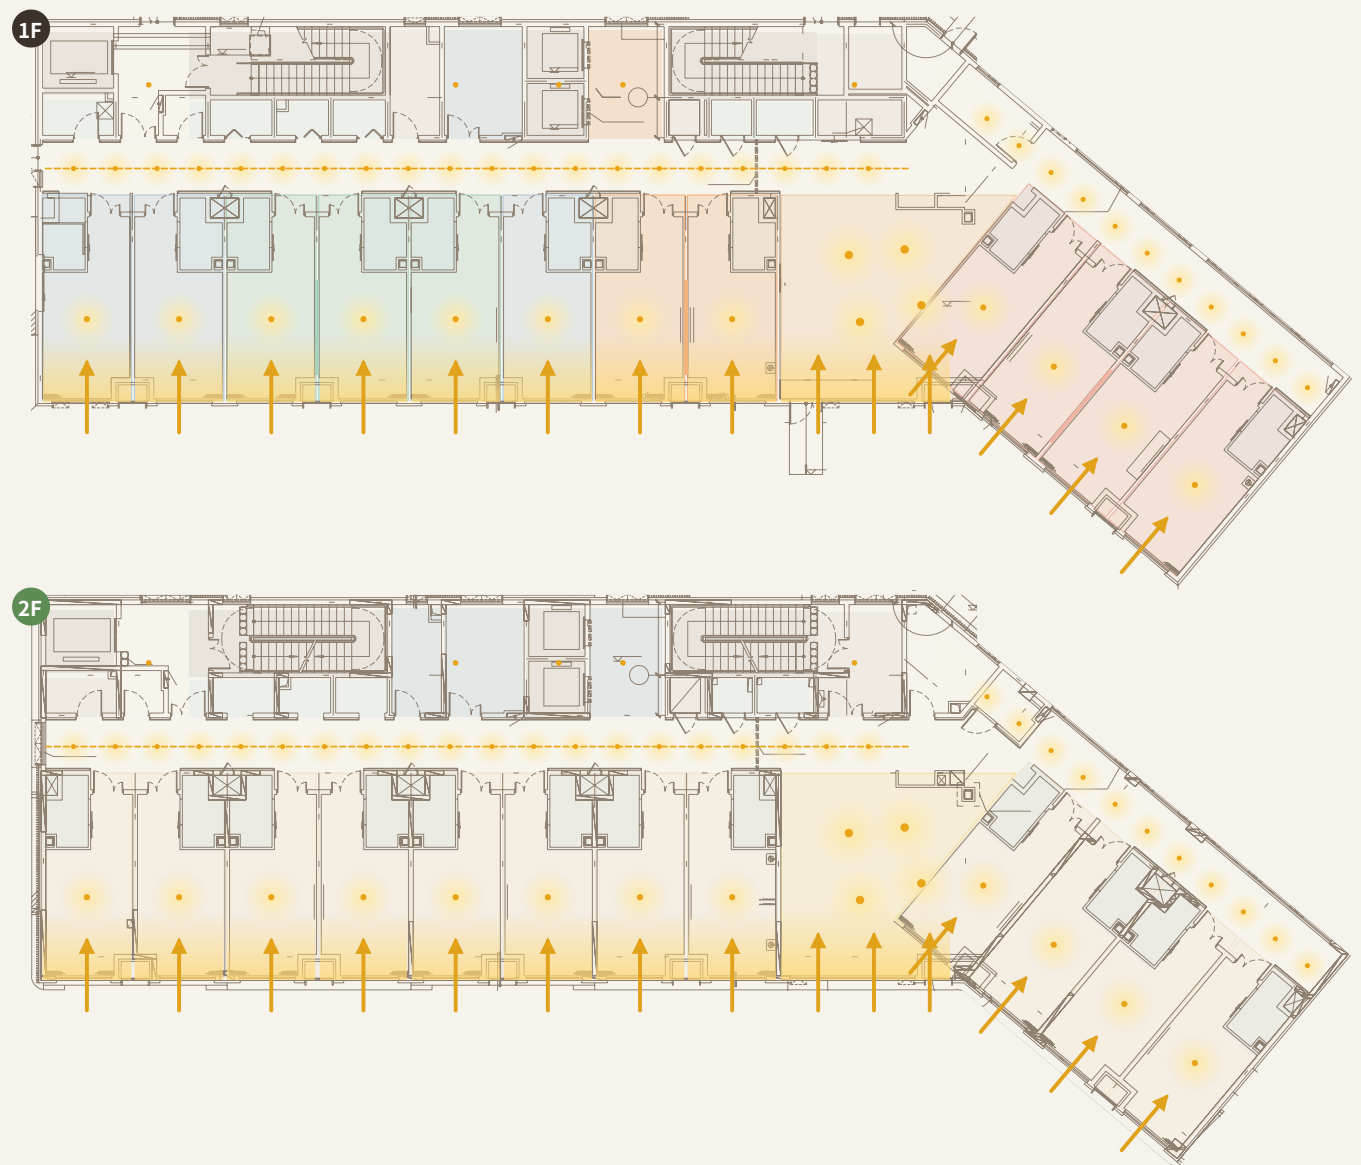

南向自然光 3000K 灯光