

一层·公共服务层

接待·康复·医护·助餐·文娱

把社区请进来，让长者走出去

一层平面图 GROUND FLOOR PLAN


1:90 · 示意



- 1 进得来 南向坡道+感应门，入口即门厅
- 2 走得稳 双侧扶手、无高差、每12m设座
- 3 愿意留 康复、食堂、活动厅连成一串
- 4 看得见 服务空间玻璃隔断，视线通透


策略分析 DESIGN ANALYSIS

功能分区 ZONING

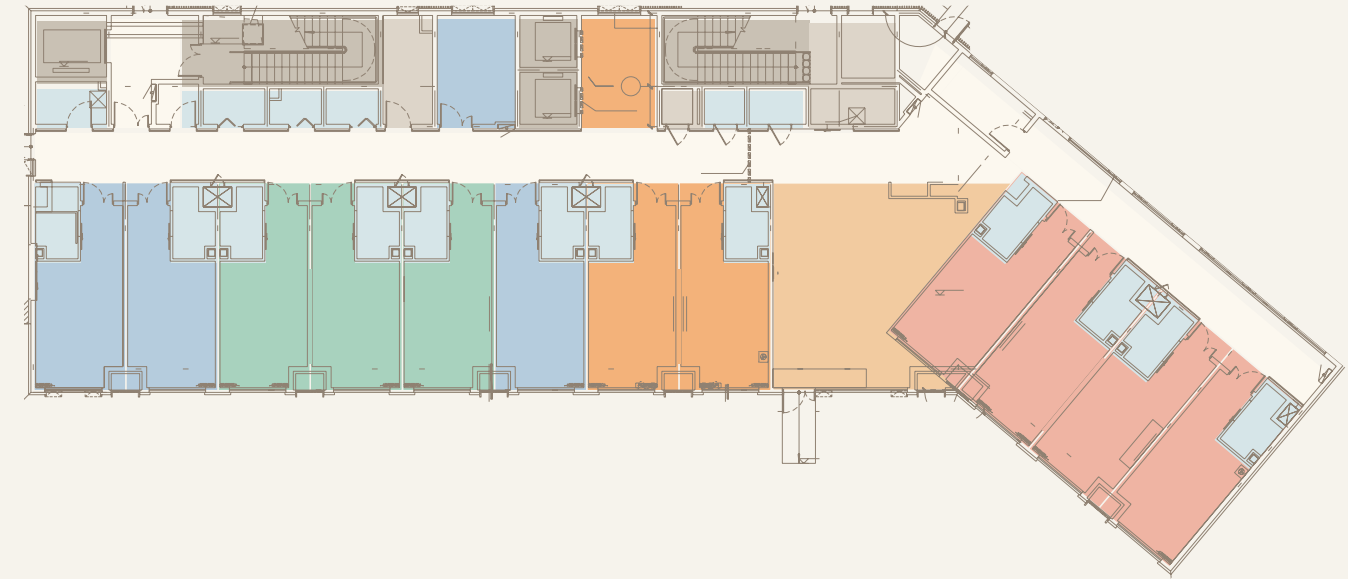


接待·门厅 餐饮·备餐 康复·理疗 医护·健康 文娱·活动 后勤·辅助

动线 CIRCULATION

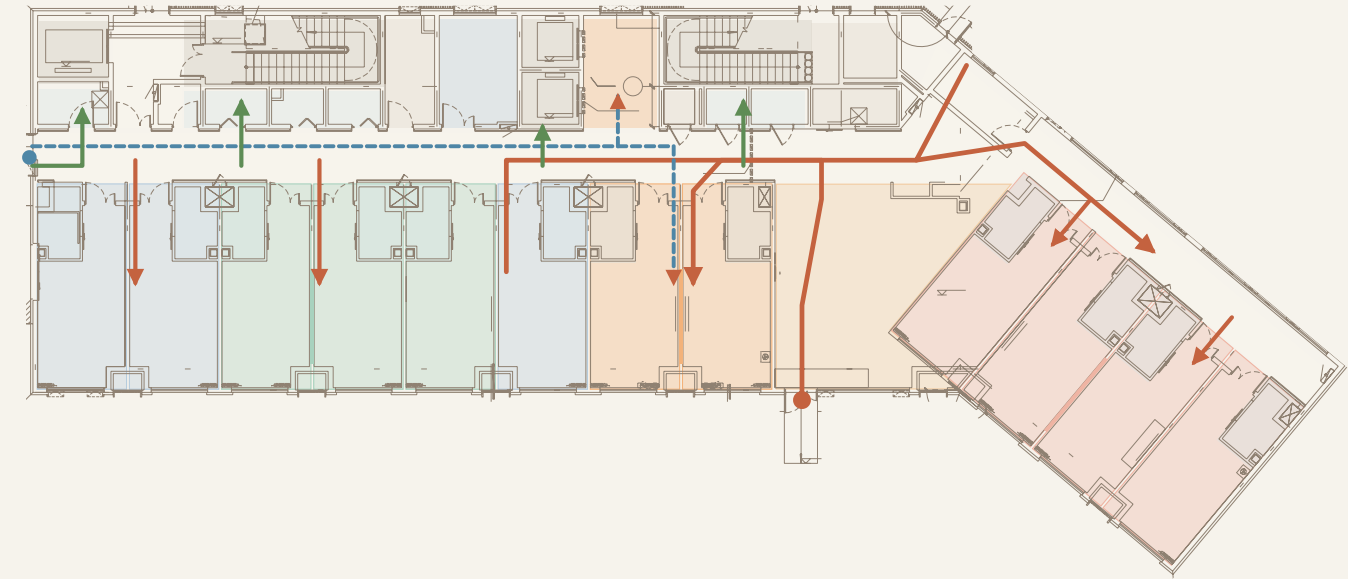

长者/访客 后勤服务 垂直交通

无障碍与安全 ACCESSIBILITY

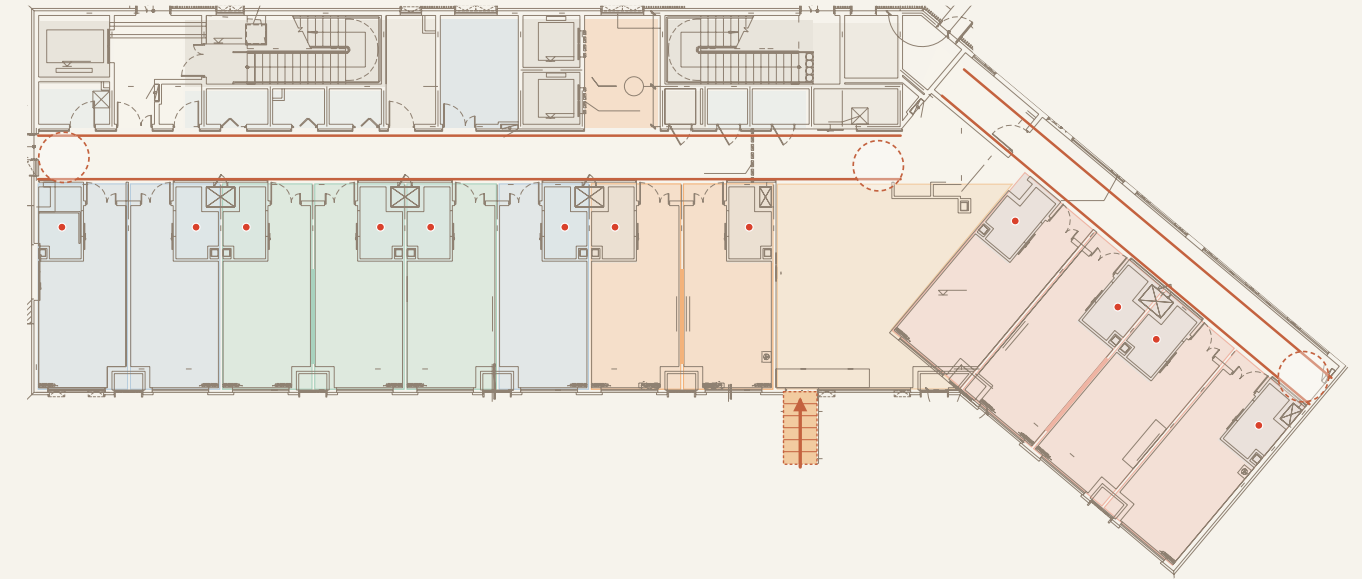

双侧扶手 回转Ø1.8m 呼叫点

重点空间 KEY SPACES



康复训练室 REHAB GYM

平行杠、落地镜、肋木；两开间约47㎡，可同时6-8人训练



长者食堂·助餐 CANTEEN

圆桌6人×3共18座；圆椅带扶手，热食备餐间紧邻




多功能活动厅 ACTIVITY HALL

书画、影院、棋牌三室连片，转角翼40°斜向成“街角”

面积表 SCHEDULE · ㎡

01 值班·安防	23.6	06 长者食堂·助餐	47.2
02 健康小屋·医务	23.6	07 门厅·接待·茶座	43.9
03 康复训练室	47.2	08 书画·手工坊	23.6
04 中医理疗室	23.6	09 多功能活动厅	47.2
05 心理·谈话室	23.6	10 棋牌·阅览	23.6
		无障碍厕所	3.5
		公共卫生间	9.3
		更衣·库房	6.8

节点详图 DETAILS

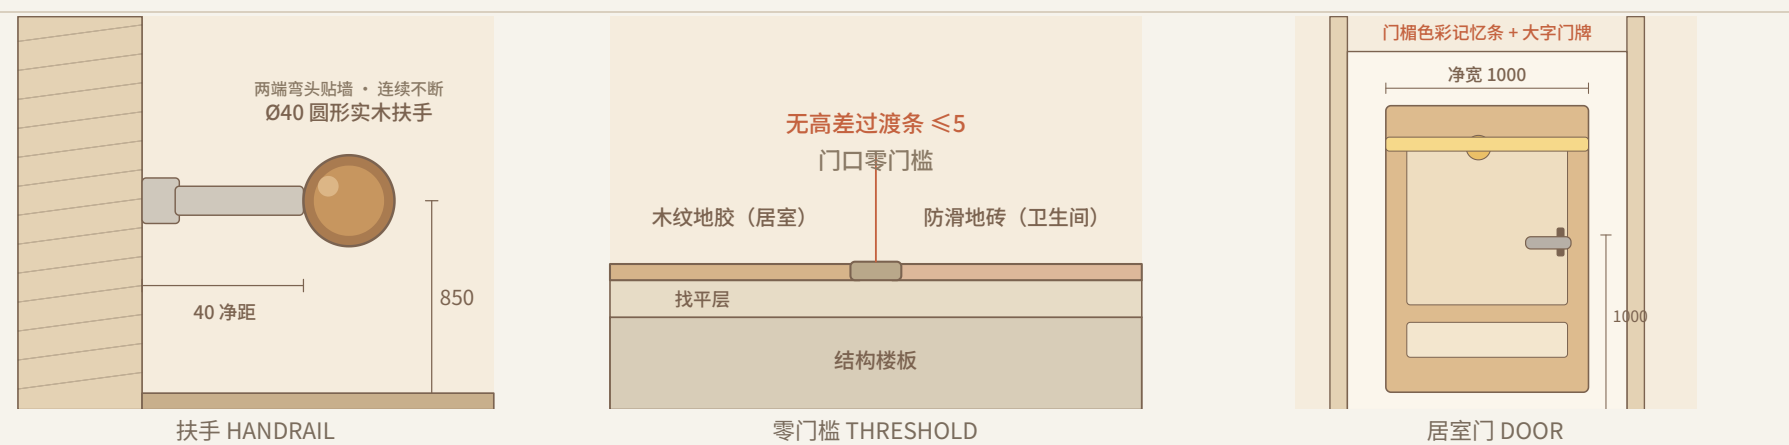

走廊双侧 650 / 850 连续扶手；所有交接位置无高差，红色对比色提示；公共区 3000K 低眩光照明。