



一层 · 公共服务层

接待 · 康复 · 医护 · 助餐 · 文娱
把社区请进来，让长者走出去

接待 · 门厅 医护 · 健康 康复 · 理疗 餐饮 · 备餐 文娱 · 活动 后勤 · 辅助 功能用房约 327㎡

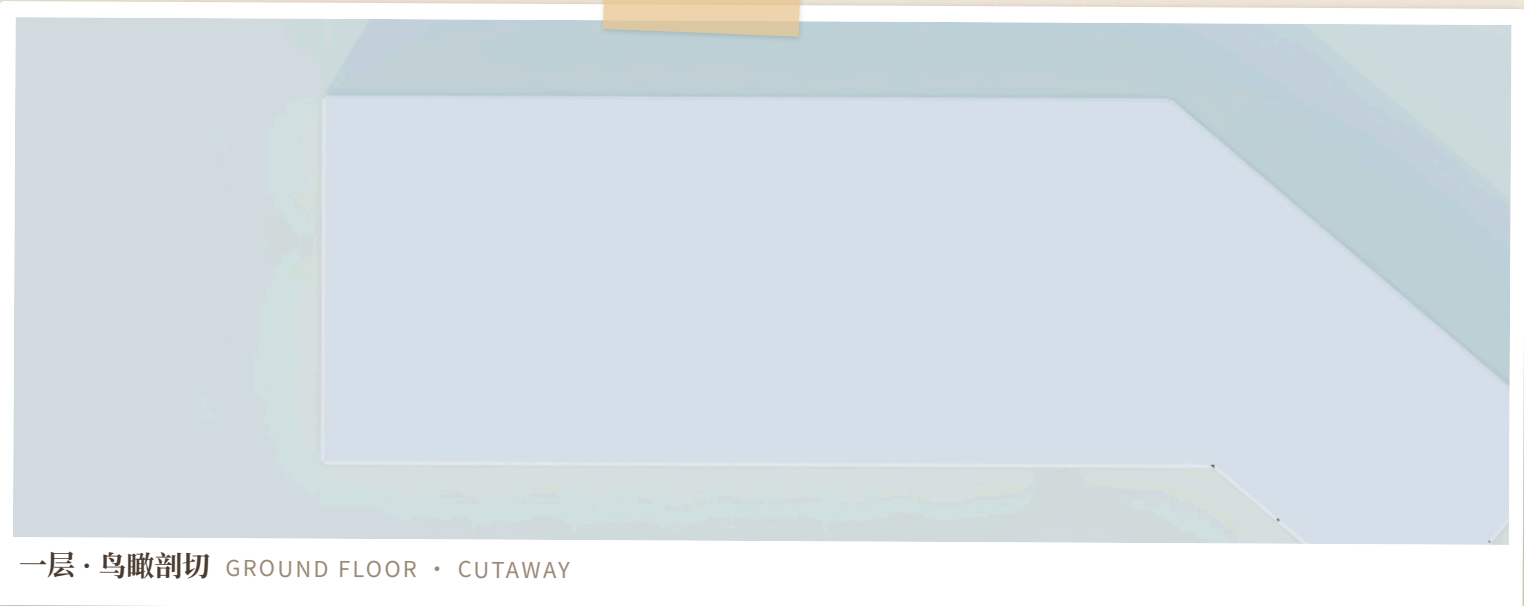

一层 · 鸟瞰剖切 GROUND FLOOR · CUTAWAY

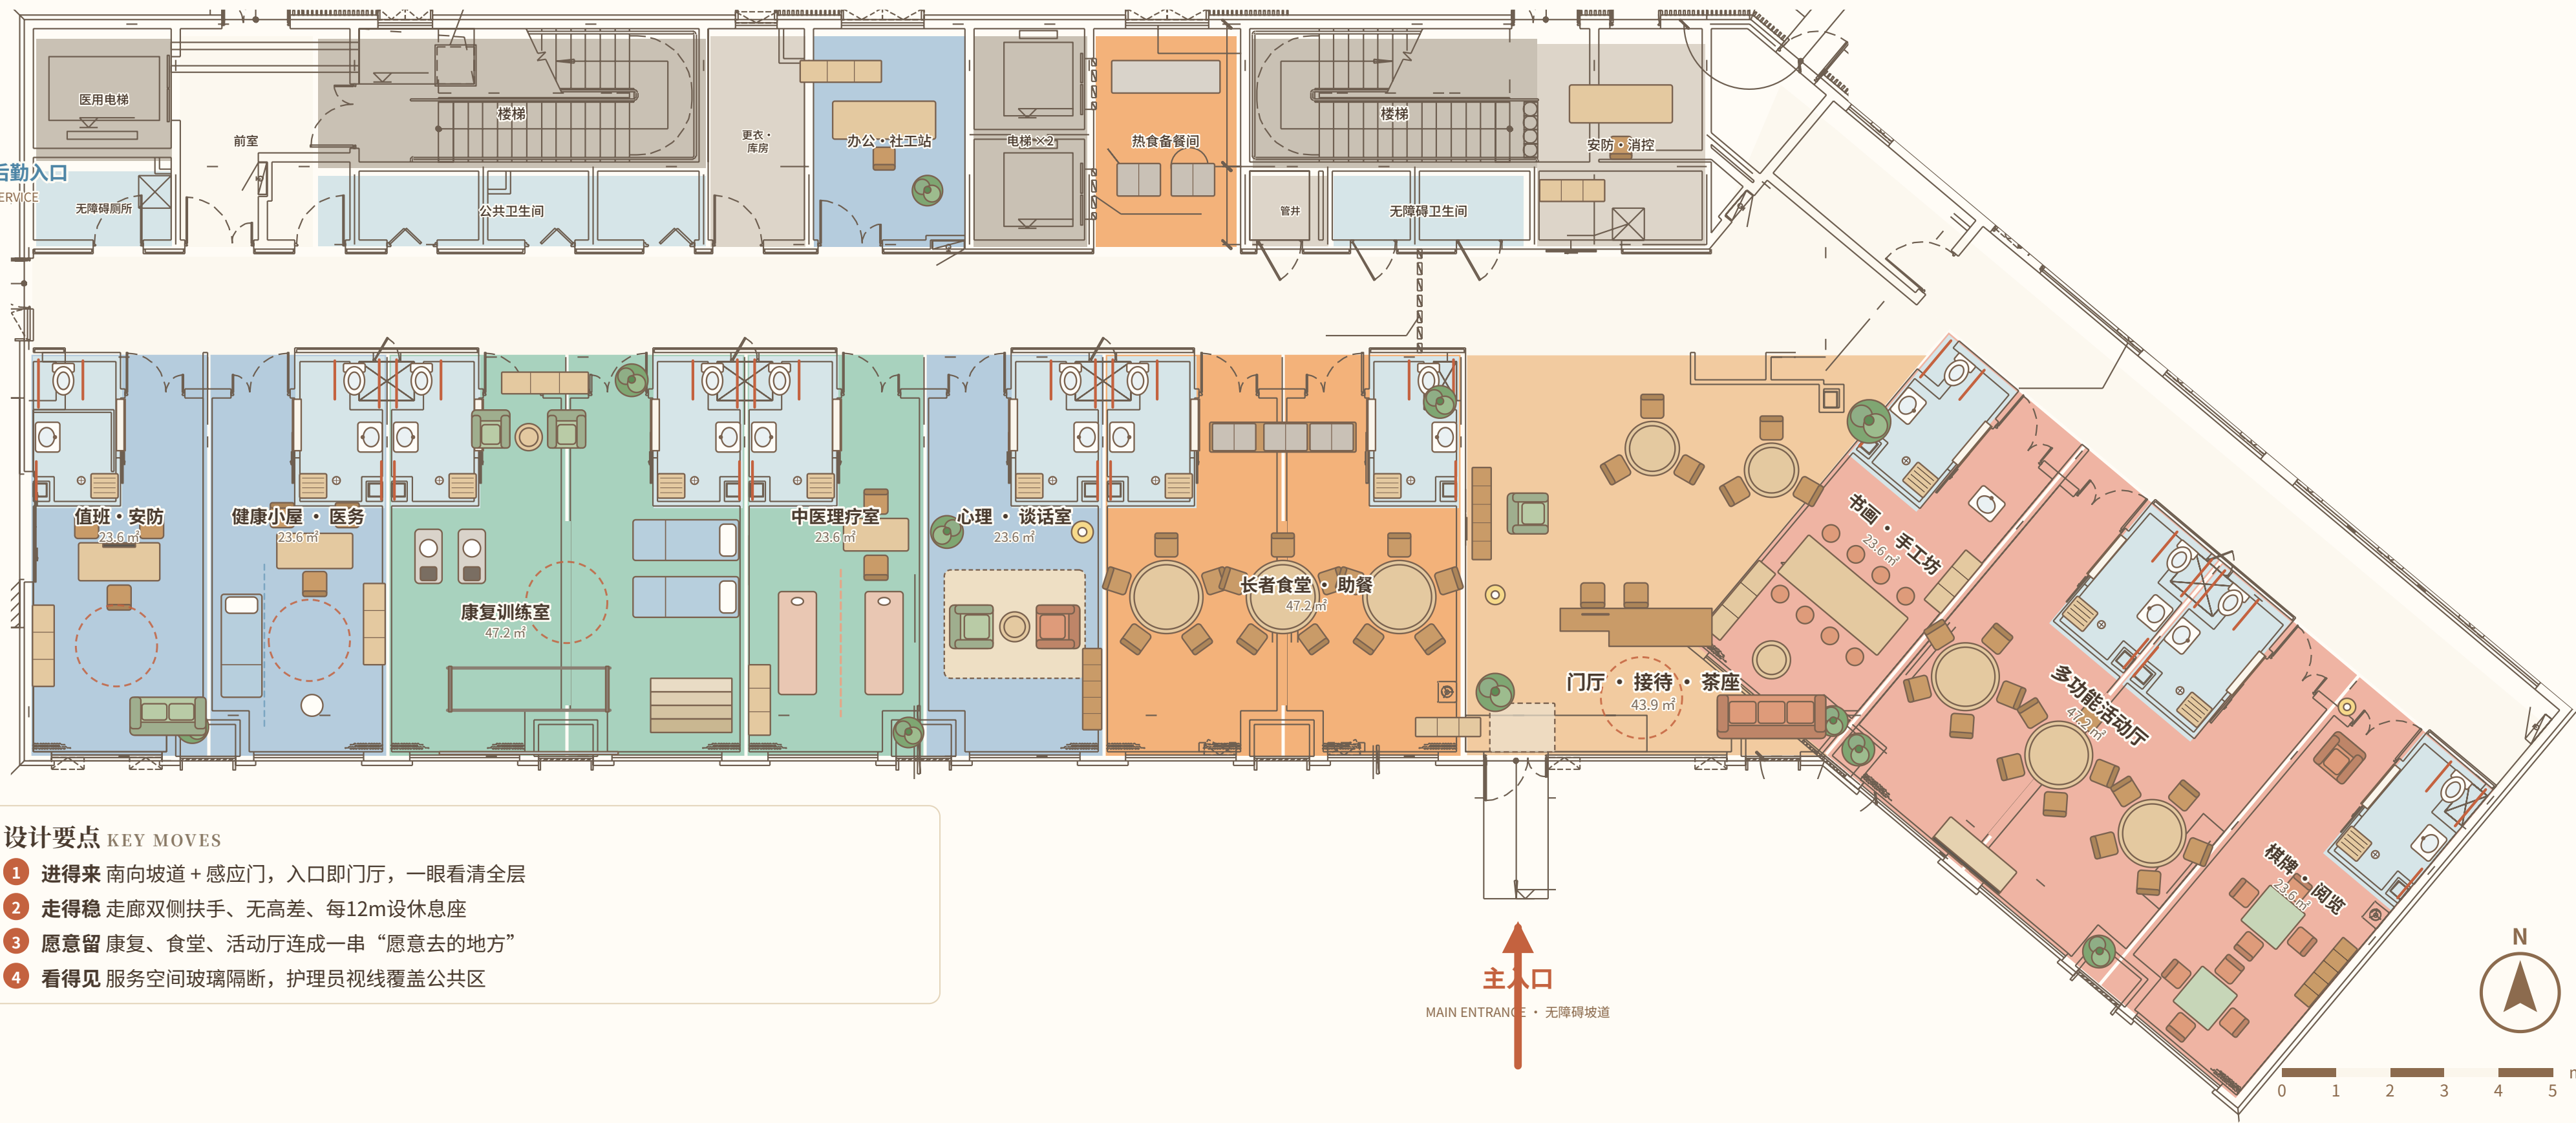


设计要点 KEY MOVES

- 进得来 南向坡道 + 感应门，入口即门厅，一眼看清全层
- 走得稳 走廊双侧扶手、无高差、每12m设休息座
- 愿意留 康复、食堂、活动厅连成一串“愿意去的地方”
- 看得见 服务空间玻璃隔断，护理员视线覆盖公共区

一层平面图 GROUND FLOOR PLAN 1:90 (示意，随排版比例)


A 功能分区

ZONING

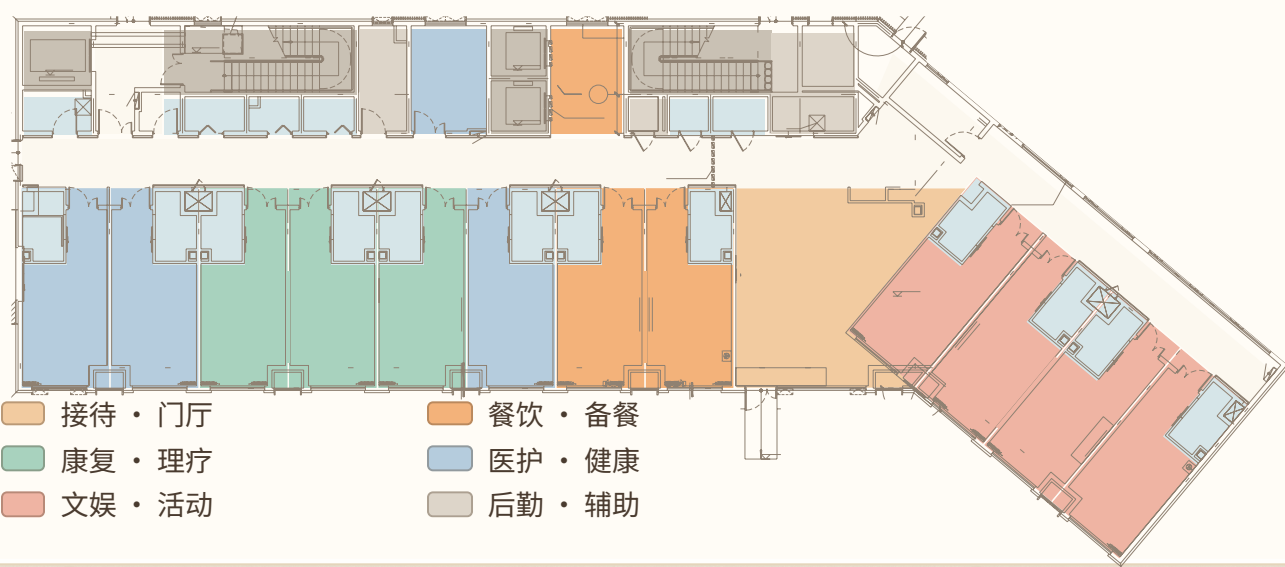


B 动线分析

CIRCULATION

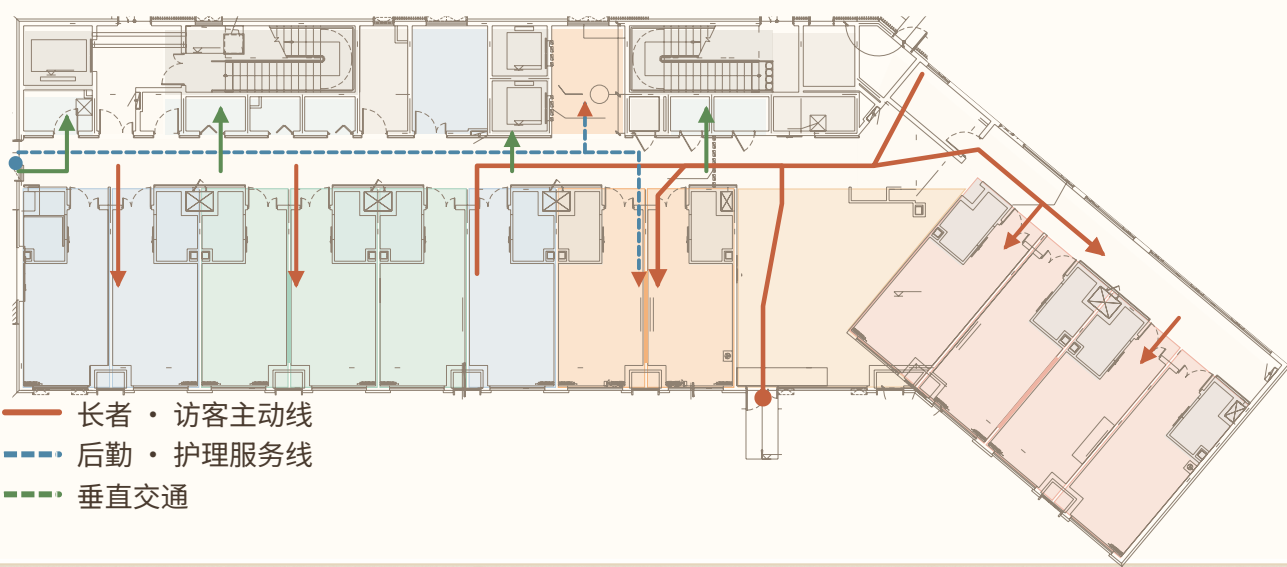


C 无障碍与安全

ACCESSIBILITY

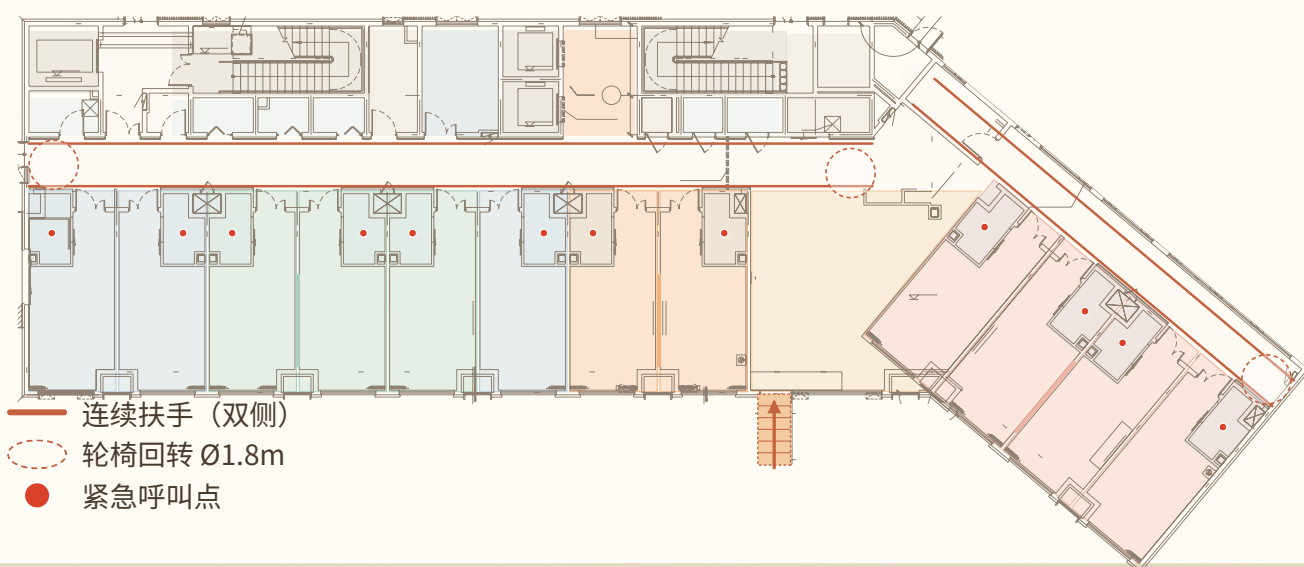

1 门厅 · 接待 · 茶座

LOBBY & TEA LOUNGE

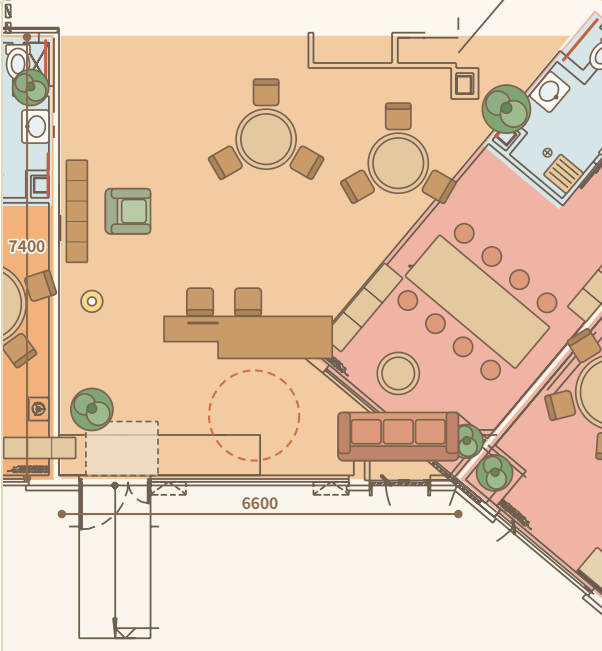



- 低位接待台一半 750mm，轮椅可近，可坐着服务
- 无高差入口：南向 1:12 缓坡 + 感应门净宽 ≥1200
- 日光茶座面向廊道，长者“看得见来往的人”

门厅 · 接待 LOBBY

进门就暖

2 康复训练室

REHAB GYM

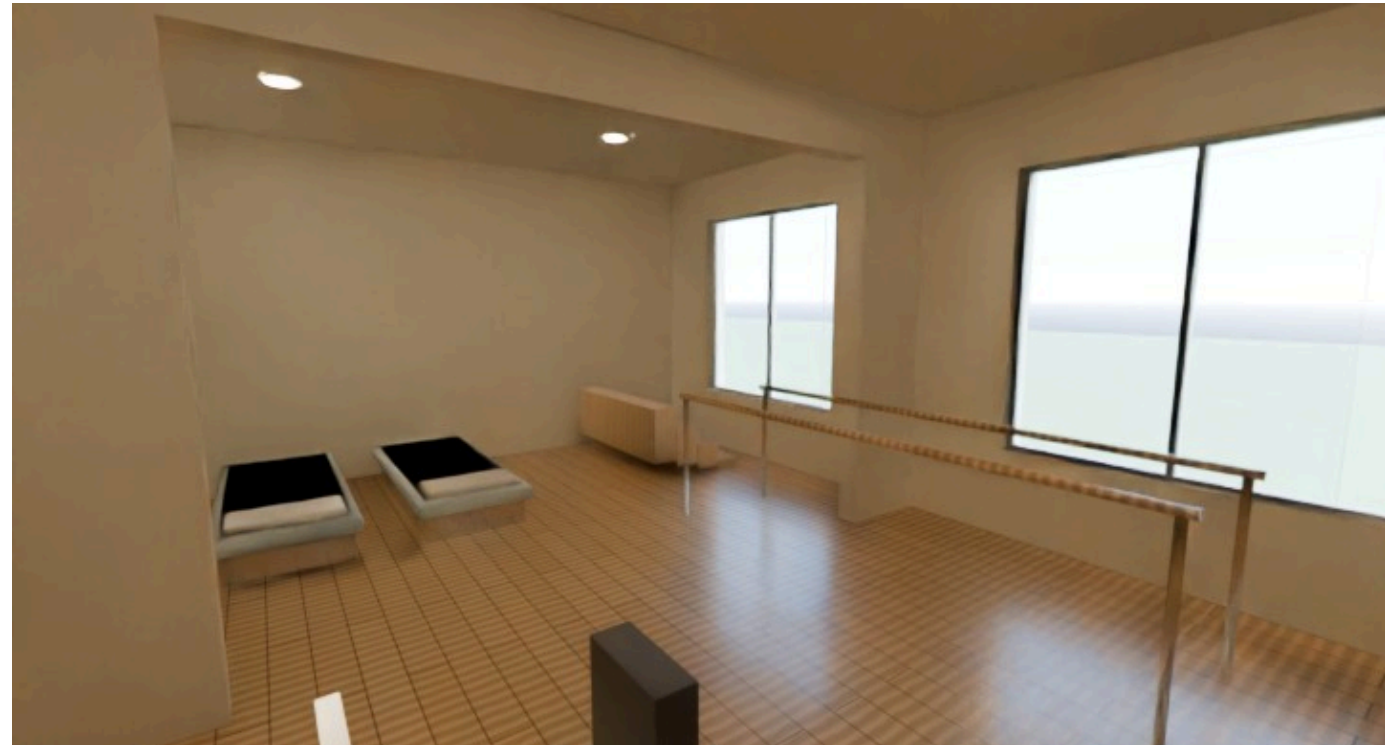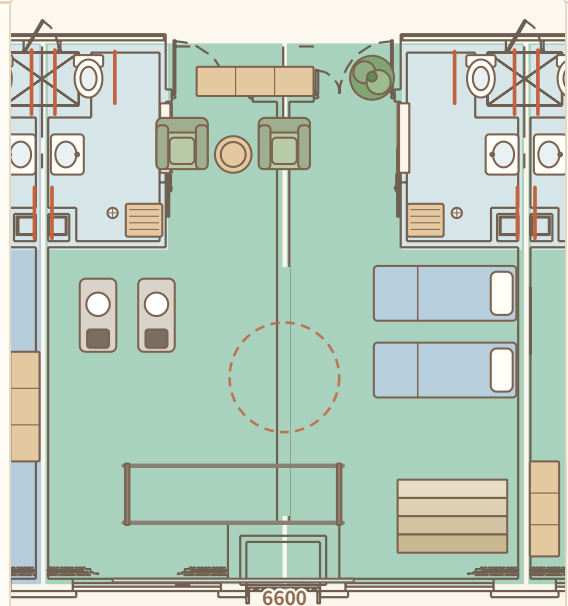


- 步行训练区：平行杠 + 落地镜；肋木、PT 训练床
- 两开间打通，约 47㎡，可同时 6-8 人训练
- 弹性防滑地胶，墙面 0.9m 起扶手贯通

康复训练 REHAB

动一动更好

3 长者食堂 · 助餐

COMMUNITY CANTEN

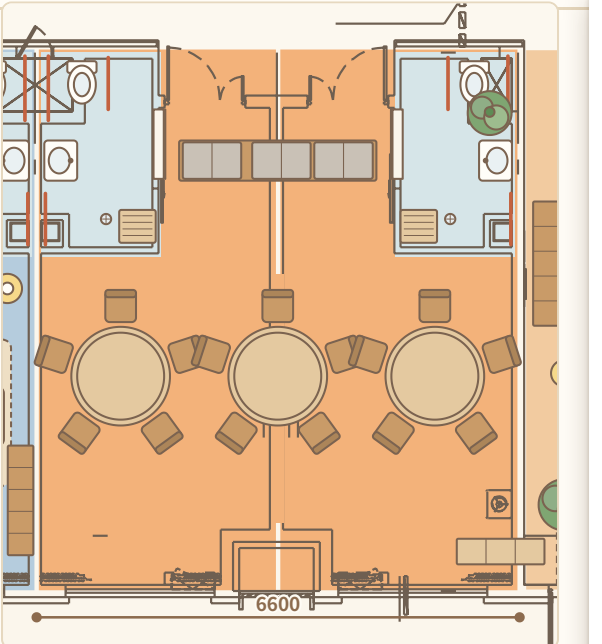



- 圆桌 6 人 × 3 = 18 座，圆椅带扶手，桌下净高 ≥700
- 助餐台 + 保温柜 + 洗消，热食备餐间紧邻
- 餐时错峰 · 助餐员一对一服务

长者食堂 CANTEN

热乎的一顿饭

4 多功能活动厅群

ACTIVITY WING

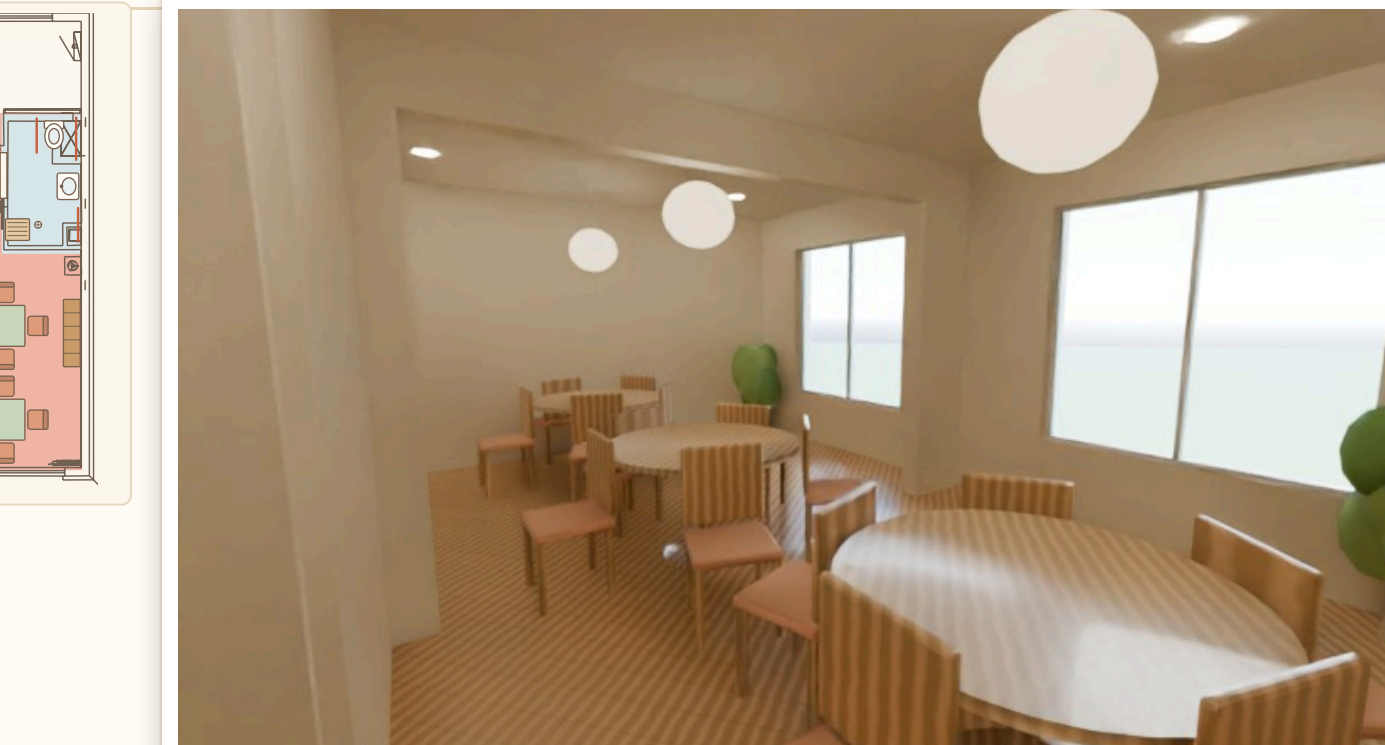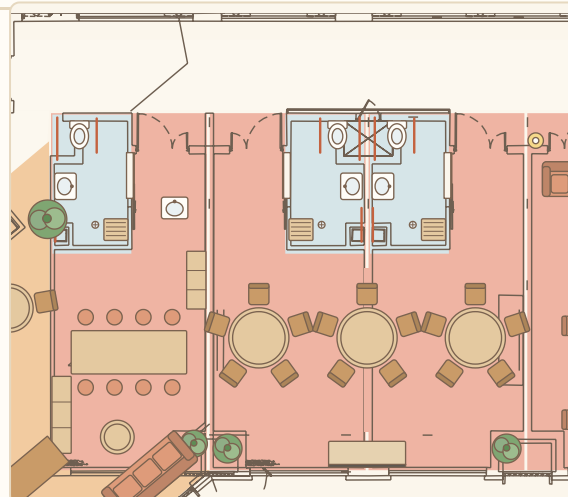

- 书画 / 怀旧影院 / 棋牌三室连片，可整体打开
- 转角翼 40° 斜向，形成有变化的“街角”感
- 暖黄灯光 + 岁月留影墙，唤起共同记忆

活动厅 ACTIVITY HALL

热闹的小街角

5 面积表

SCHEDULE · ㎡

功能用房	㎡	服务 · 交通	㎡
01 值班 · 安防	23.6	无障碍厕所	3.5
02 健康小屋 · 医务	23.6	公共卫生间	9.3
03 康复训练室	47.2	更衣 · 库房	6.8
04 中医理疗室	23.6	办公 · 社工站	10.9
05 心理 · 谈话室	23.6	热食备餐间	10.1
06 长者食堂 · 助餐	47.2	无障碍卫生间	4.5
07 门厅 · 接待 · 茶座	43.9	安防 · 消控	11.6
08 书画 · 手工坊	23.6		
09 多功能活动厅	47.2		
10 棋牌 · 阅览	23.6		

医护 · 健康 71㎡ · 22% 康复 · 理疗 71㎡ · 22% 餐饮 · 备餐 47㎡ · 14% 接待 · 门厅 44㎡ · 13% 文娱 · 活动 94㎡ · 29%

6 节点详图

DETAILS



地面

- 木纹防滑地胶 · 无缝
- 走廊双侧 650 / 850 两道连续扶手，端部弯头贴墙
- 公共区照明 3000K、低眩光；接待台、台阶边缘增设对比色

墙面

艺术涂料 + 0.9m 橡木墙裙

顶部

白色乳胶漆 + 线性灯带

- 所有交接位置 无高差，过渡条 ≤5mm，红色对比条提示
- 大厅、走廊设 休息座椅 每 ≤12m 一处，便于老人歇脚