

二层 · 居住照护层

12 间朝南居室 · 日光起居厅 · 护理站 · 助浴
回到家，回到自己的房间

12 间单人居室 23.6 m²/间 43.9 m² 日光厅 1.8 m 中廊



二层·鸟瞰剖切 UPPER FLOOR · CUTAWAY




设计要点 KEY MOVES

- 1 朝南居室 每间都有南向与 0.6m 低窗台，坐着也能看院景
- 2 廊下有座 走廊每 12m 设一处廊下座，门旁有“记忆盒”
- 3 护理居中 护理站居走廊中部，转角翼另设护理小站与呼叫中继
- 4 日光起居 东端大厅朝南，是全层的客厅与餐厅


二层平面图 SECOND FLOOR PLAN 1:90 (示意，随排版比例) · 黄色箭头：南向自然光

A 寻路与记忆


WAYFINDING

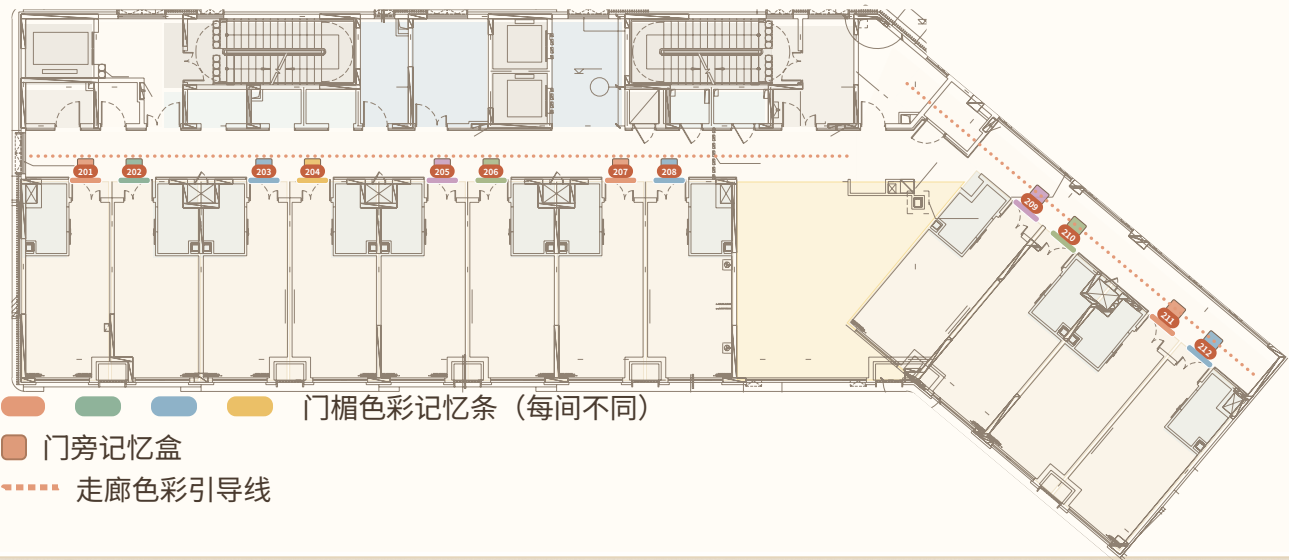

1 标准居室 (镜像成对)

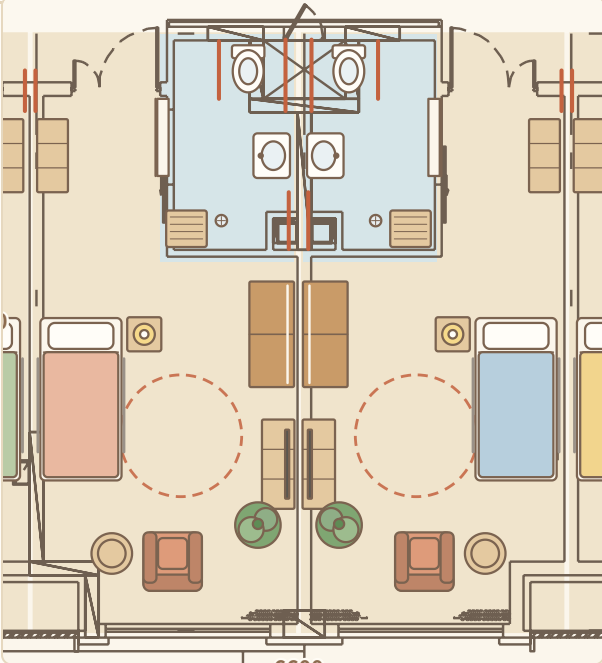


标准居室平面 (201-202 镜像)

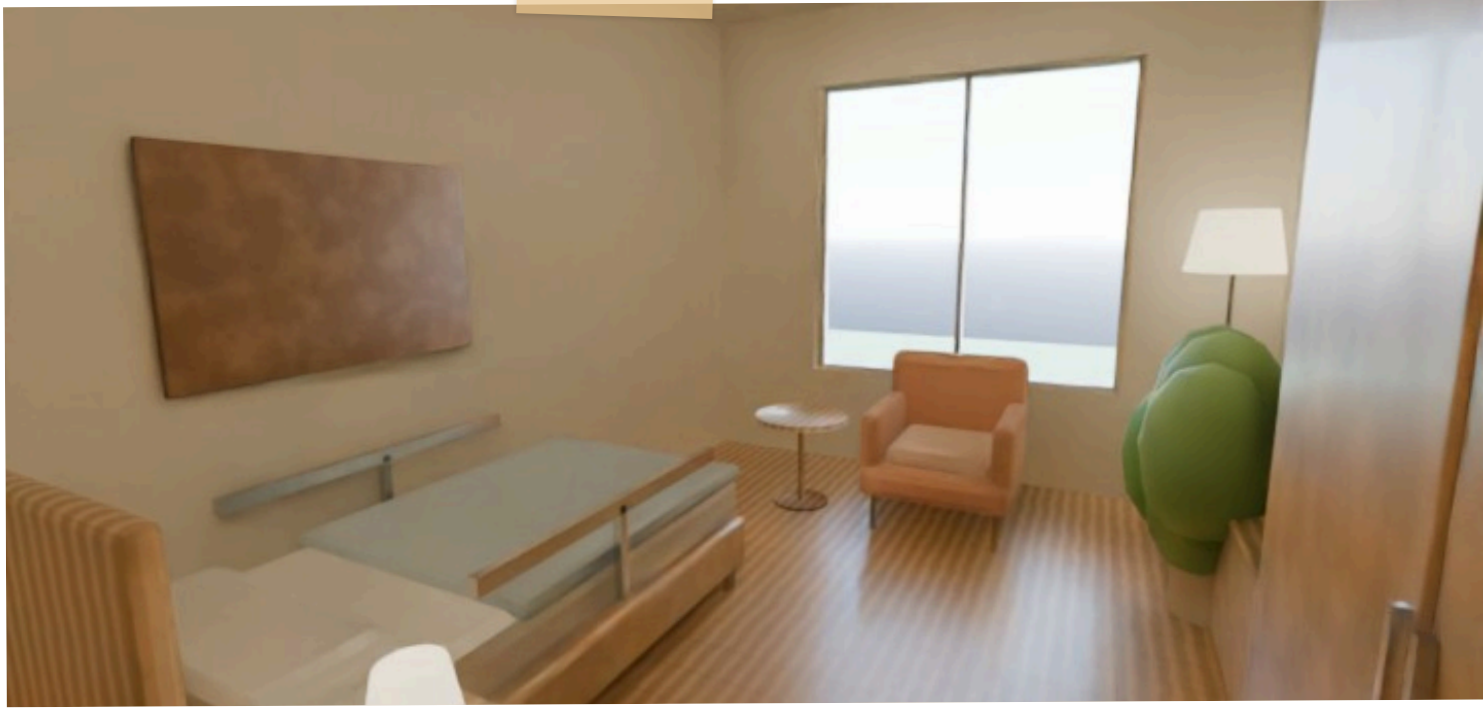

居室·我的小家 TYPICAL ROOM

窗前晒太阳

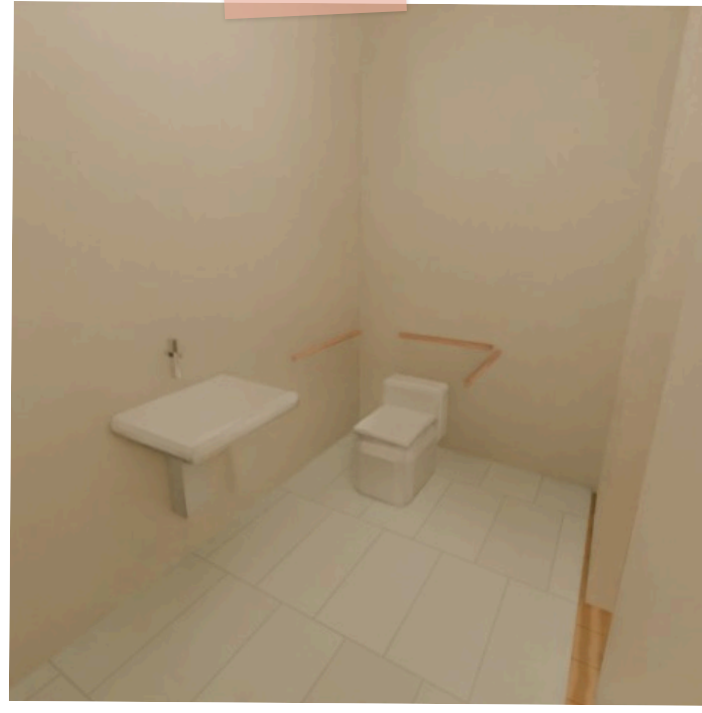


无障碍卫生间 ACCESSIBLE BATH

- 床：电动护理床 1000×2000，床头靠实墙，一侧留 ≥1200 供轮椅转移
- 床头：壁灯 + 拉绳呼叫 + 夜灯；床头柜圆角、抽屉带扶把
- 床→卫生间：脚灯 (0.25m) 连通，推拉门零门槛，路径 ≤3m
- 卫生间 1.7×2.9m：折叠淋浴座椅、L 形 + 竖向扶手、地漏中置、防眩镜灯
- 窗前：低窗台 0.6m + 扶手椅 + 边几，是老人“看世界”的位置
- 收纳：衣柜推拉门，把手在 0.9-1.1m

TYPICAL ROOM · 23.6m²

2 日光起居 · 共享餐厅

SUNLIT LIVING & DINING

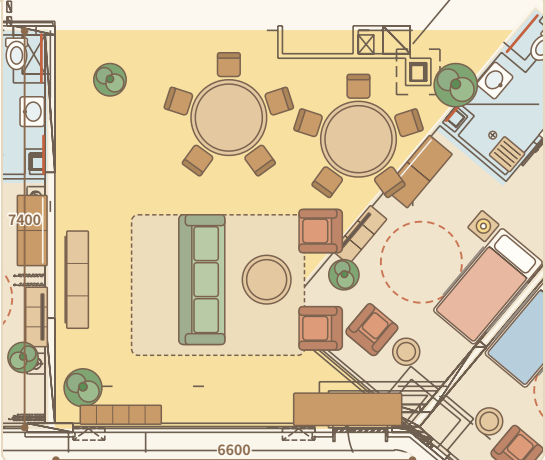

- 三级社交梯度：居室 → 廊下座 → 日光厅
- 南向大窗 + 低窗台，整日晒太阳、看街景
- 沙发座高 450、带扶手，起身不费力
- 茶水台兼护理小站，视线覆盖大厅




日光厅 LIVING & DINING

全天有光

3 记忆走廊

MEMORY CORRIDOR

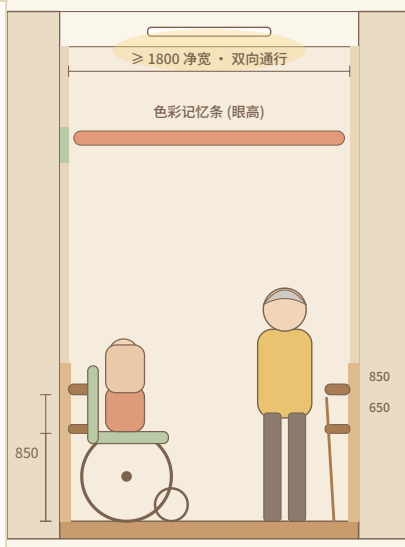

- 色彩记忆条：门楣 6 色循环，眼高位置
- 记忆盒：门旁壁龛，放老照片与小物
- 廊下座：每 ≤12m 一处，扶手连续



走廊·望得到尽头 CORRIDOR

认得出自己的门


4 居室家具设备清单

FURNITURE · PER ROOM

名称	规格 mm	数量	备注
电动护理床	1000×2000×500 可调	1	带护栏 · 呼叫器
床头柜	450×450×550	1	圆角 · 夜灯
衣柜 (推拉门)	1300×550×2000	1	把手 0.9-1.1m
高座扶手椅	720×720×900	1	座高 450
圆边几	Ø500×500	1	软包边
电视柜 + 电视	1100×400	1	壁挂 · 遥控
落地灯 (暖光)	Ø300×1500	1	3000K
折叠淋浴座椅	450×450	1	座高 450
L 形 / 竖向扶手	Ø40	3-4	卫生间 · 床边
呼叫器 + 拉绳	床头 + 卫生间	2	双回路 · 应急
记忆盒 (门旁)	300×350×120	1	壁龛 · 可换

5 走廊墙面


CORRIDOR ELEVATION

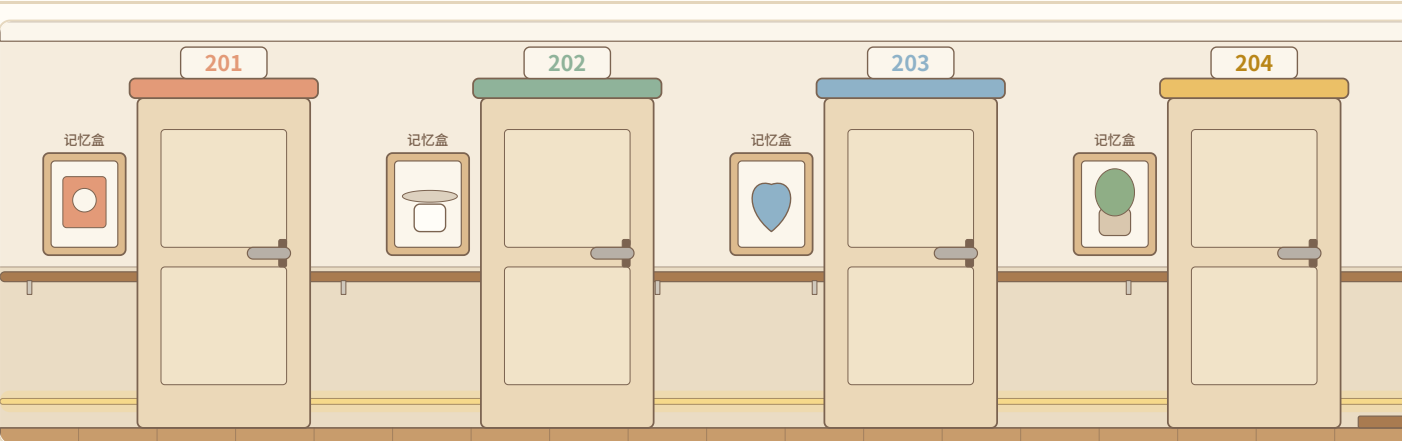

- 门楣色彩 + 记忆盒 + 大字门牌
- 走廊净宽约 1.8m，双侧连续扶手 650 / 850
- 地面无反光哑光地胶，避免暗色块 (易被误认为台阶)
- 走廊端景为窗 / 绿植 / 挂画，形成路径节点

6 转角翼

CORNER WING

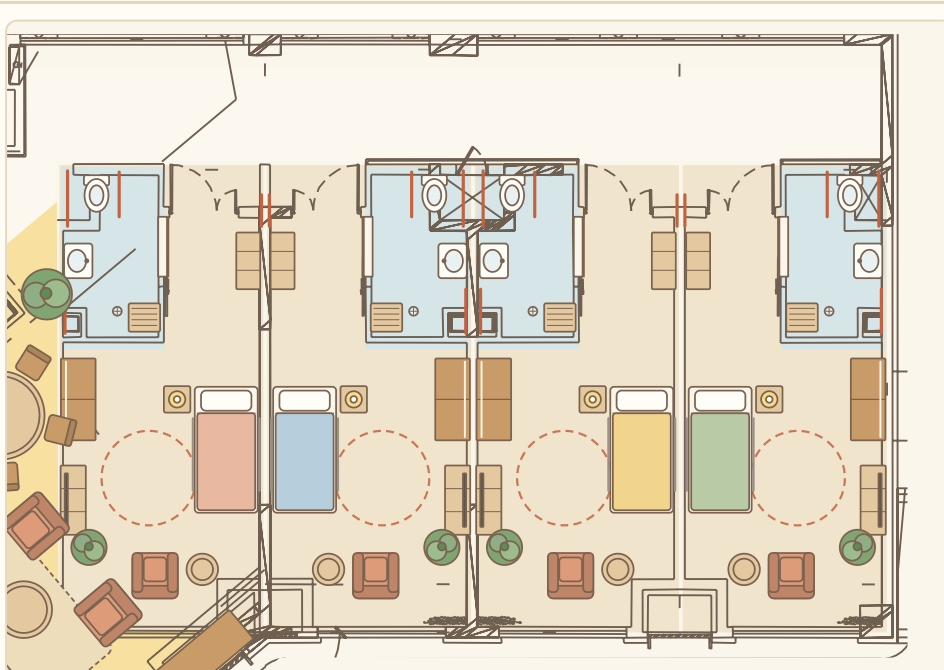

- 转角翼 4 间居室，自成“小街区”，适合认知症长者
- 走廊尽端设景观窗与休憩座，避免“死胡同”
- 每间门楣异色，红色引导线直达日光厅